

TICKET NUMBER	LENGTH	HEIGHT	WIDTH	THICKNESS	QUANTITY
14T-002	905	292		106	

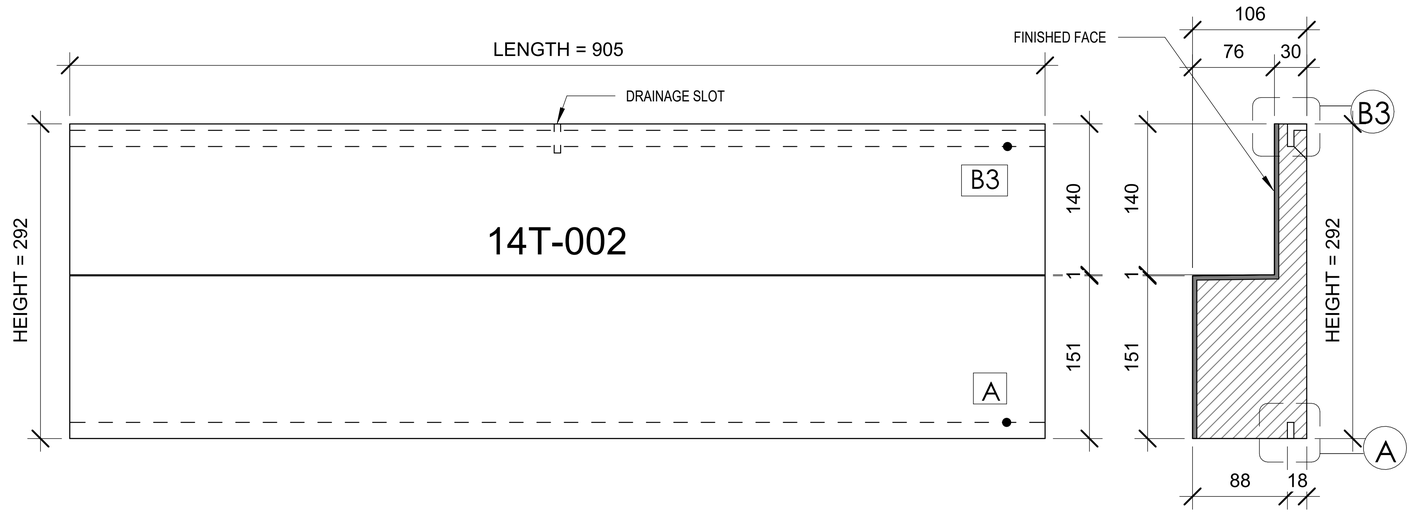


ELEVATION


SECTION

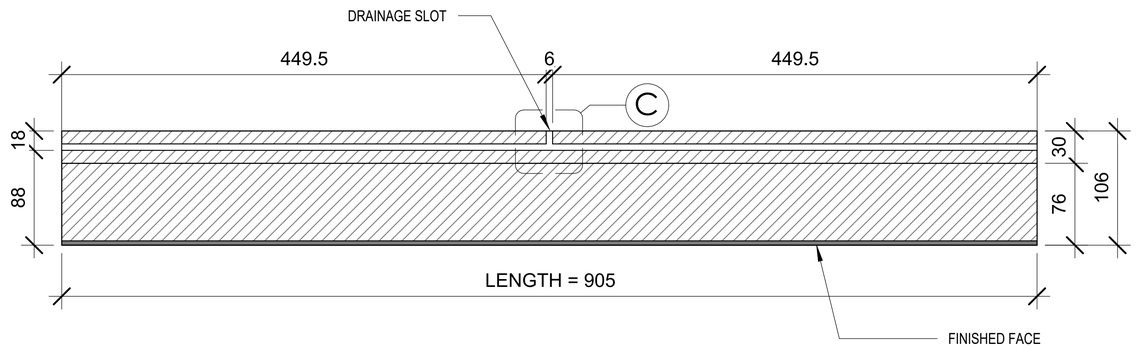


PLAN

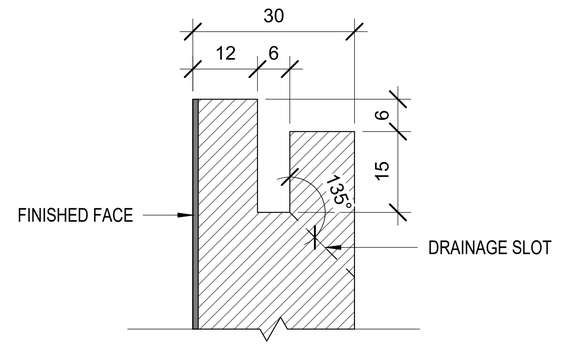

DETAIL B3 - REBATED KERF (30mm thick stone)

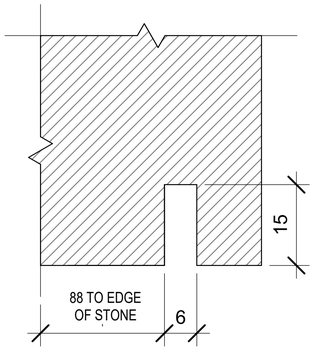

DETAIL A - KERF (thick stone)

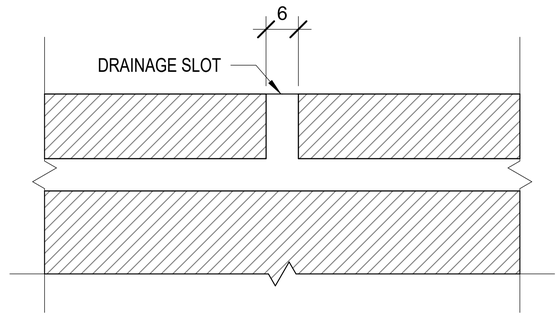

DETAIL C - DRAINAGE SLOT

Rev.	Date	By	Description
05	2025.12.19		STONE TICKET PACKAGE P6 For Production

TOLERANCE:		INHABIT GROUP	
PROJECT No:	0001	http://www.inhabitgroup.com	
CLIENT:	ECLAD	© Copyright	
DRAWN BY:	Natthapol K.	CHECKED BY:	Dararat P.
SCALE:	Not To Scale	DATE:	19/12/25

MATERIAL:	Blanco Cristal	FINISH:	Honed
PROJECT:	VANCOUVER WASHINGTON TEMPLE		
TICKET NUMBER:	14T-002	REVISION:	00