

TICKET NUMBER	LENGTH	HEIGHT	WIDTH	THICKNESS	QUANTITY
19T-003	960	395		73	

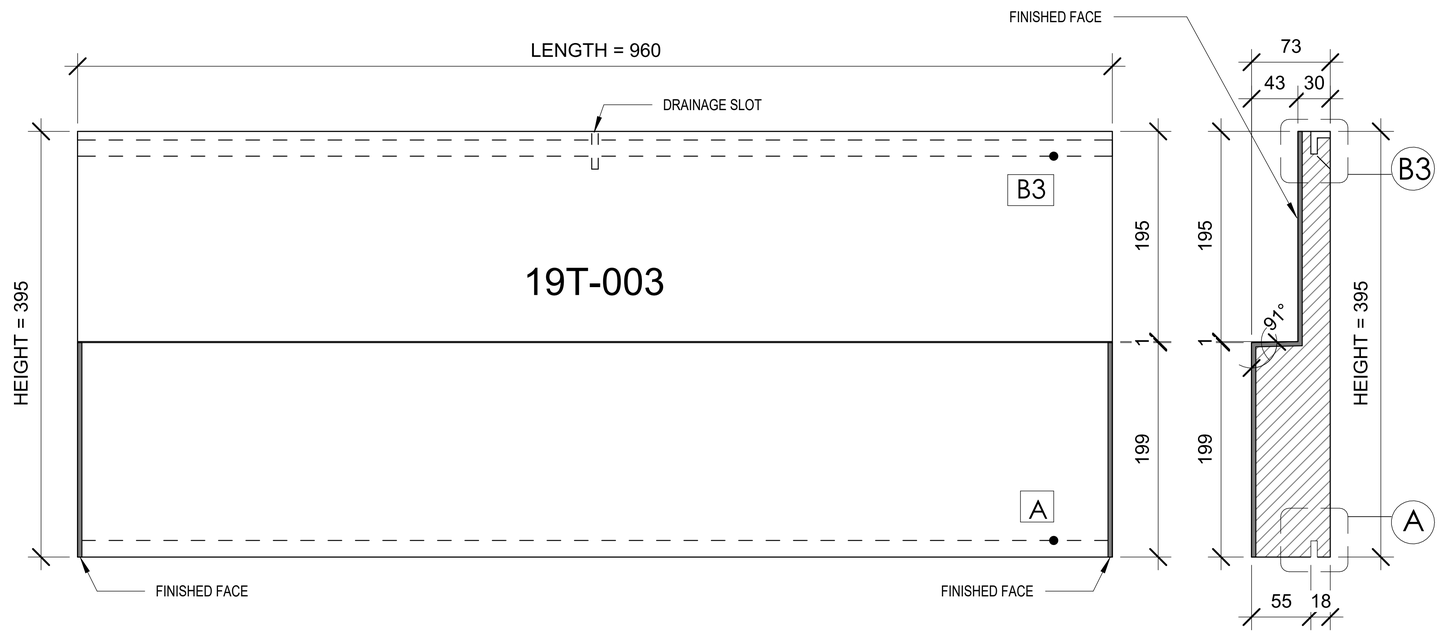


ELEVATION


SECTION

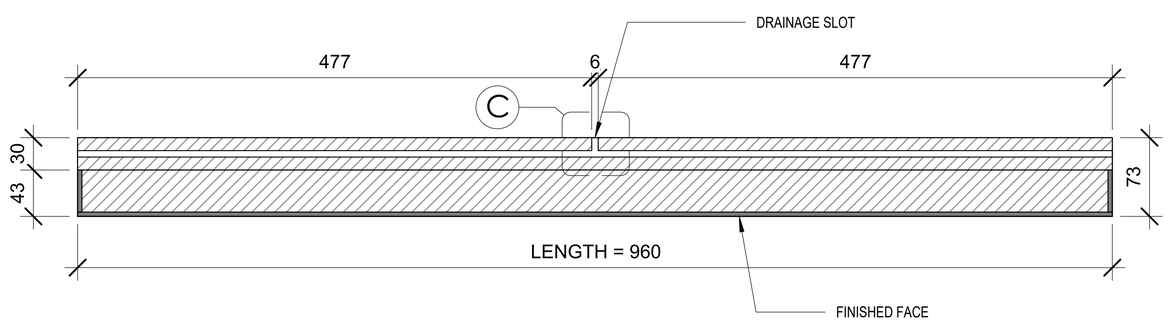


PLAN

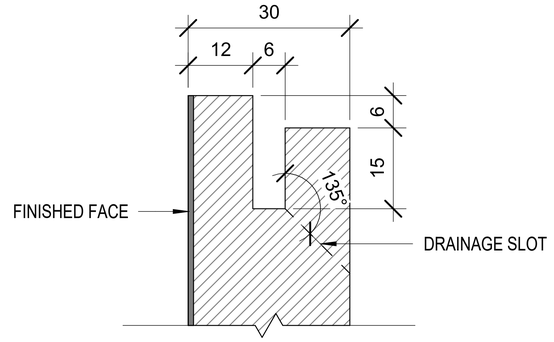

DETAIL B3 - REBATED KERF (30mm thick stone)

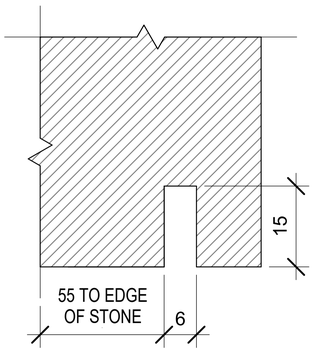

DETAIL A - KERF (thick stone)

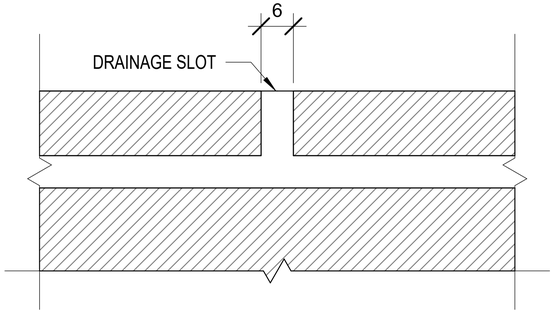

DETAIL C - DRAINAGE SLOT

Rev.	Date	By	Description
04	2025.12.04		STONE TICKET PACKAGE P5 and P7 For Production
07	2026.01.14		STONE TICKET PACKAGE P3, P4, P5 and P6 For Production

TOLERANCE:		INHABIT GROUP	
		http://www.inhabitgroup.com	
		© Copyright	
PROJECT No:	0001		
CLIENT:	ECLAD		
DRAWN BY:	Natthapol K.	**CHECKED BY:**	Dararat P.
SCALE:	Not To Scale	**DATE:**	14/01/26

MATERIAL:	Blanco Cristal	**FINISH:**	Honed
PROJECT:	VANCOUVER WASHINGTON TEMPLE		
TICKET NUMBER:	19T-003	**REVISION:**	01