


TICKET NUMBER	LENGTH	HEIGHT	WIDTH	THICKNESS	QUANTITY
1T-004	1289	248	0	124	

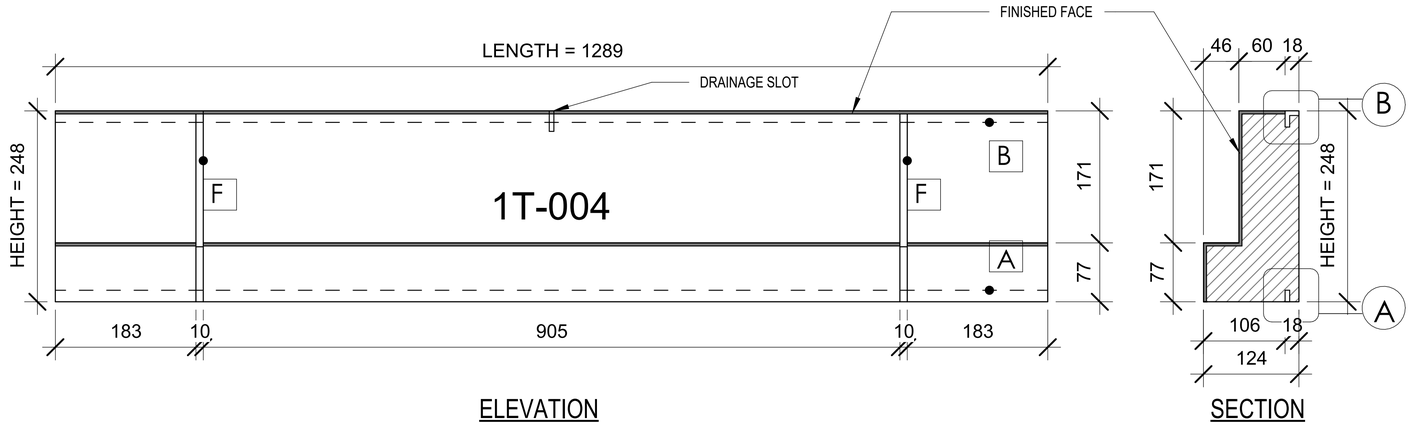


ELEVATION

SECTION

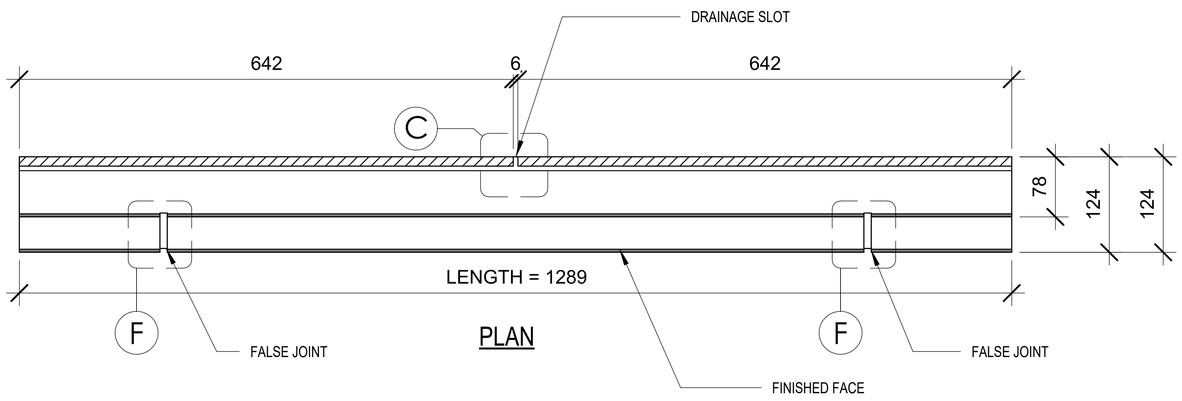


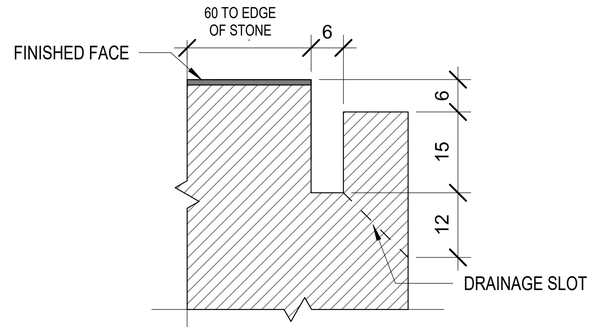


DETAIL B - REBATED KERF (thick stone)

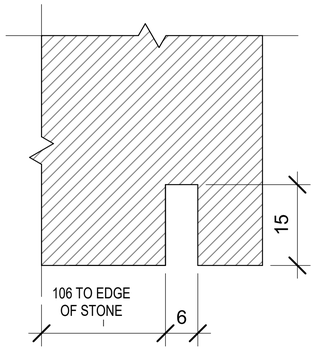

DETAIL A - KERF (thick stone)

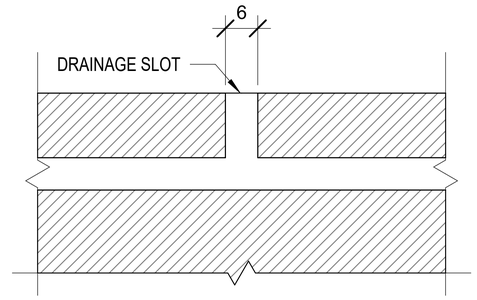

DETAIL C - DRAINAGE SLOT

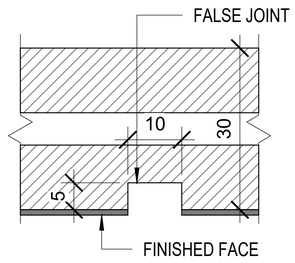

DETAIL F - FALSE JOINT

Rev.	Date	By	Description
12	2026.05.29		STONE TICKET PACKAGE P3, P4 ,P5 and P6 For Production

TOLERANCE:		INHABIT GROUP	
PROJECT No:	0001	http://www.inhabitgroup.com	
CLIENT:	ECLAD	© Copyright	
DRAWN BY:	Pattarapon P.	**CHECKED BY:**	Dararat P.
SCALE:	Not To Scale	**DATE:**	28/05/26

MATERIAL:	Blanco Cristal	**FINISH:**	Honed
PROJECT:	VANCOUVER WASHINGTON TEMPLE		
TICKET NUMBER:	1T-004	**REVISION:**	00