

TICKET NUMBER	LENGTH	HEIGHT	WIDTH	THICKNESS	QUANTITY
28T-001	905	152	0	69	

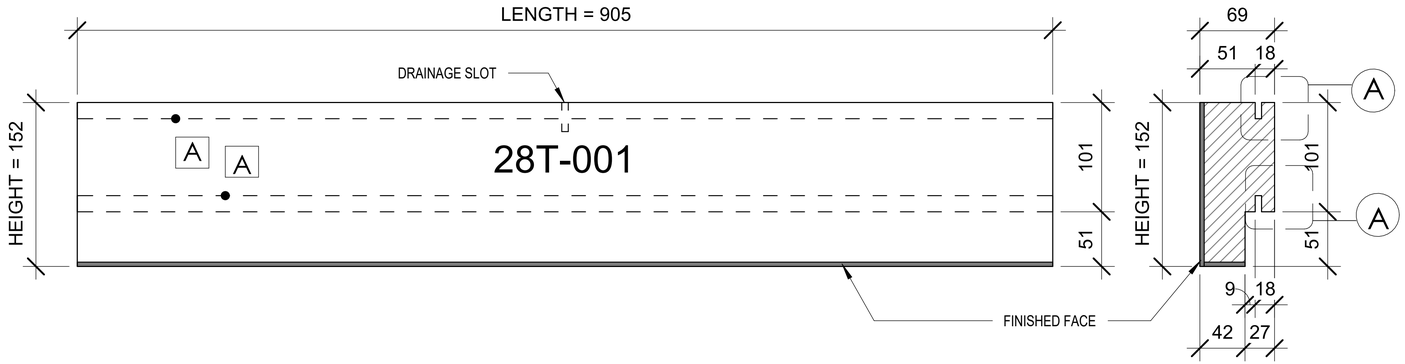


ELEVATION

SECTION


PLAN

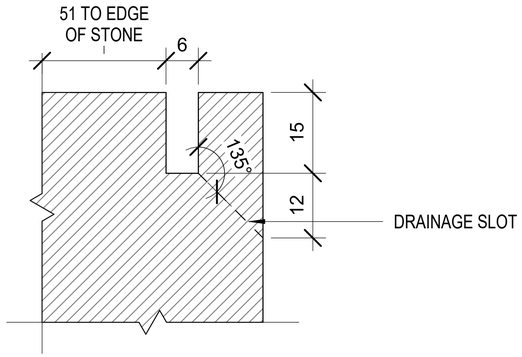

DETAIL A - KERF (thick stone)

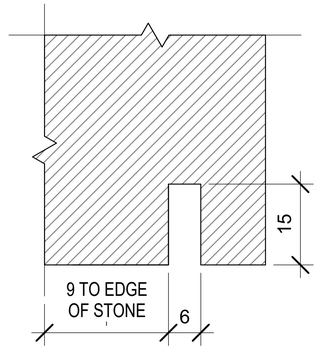

DETAIL A - KERF (thick stone)

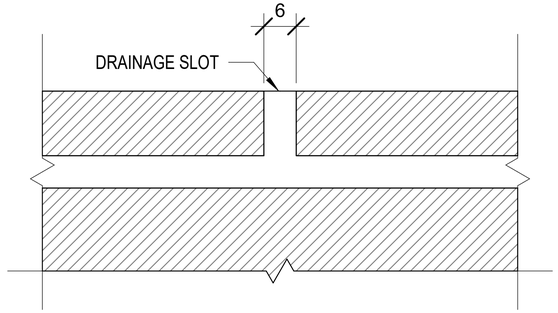

DETAIL C - DRAINAGE SLOT

Rev.	Date	By	Description
18	2026.08.27		STONE TICKET PACKAGE P8 For Production

TOLERANCE:		INHABIT GROUP	
		http://www.inhabitgroup.com	
		© Copyright	
PROJECT No:	0001		
CLIENT:	ECLAD		
DRAWN BY:	Natthapol K.	**CHECKED BY:**	Dararat P.
SCALE:	Not To Scale	**DATE:**	27/08/26

MATERIAL:	Blanco Cristal	**FINISH:**	Honed
PROJECT:	VANCOUVER WASHINGTON TEMPLE		
TICKET NUMBER:	28T-001	**REVISION:**	00