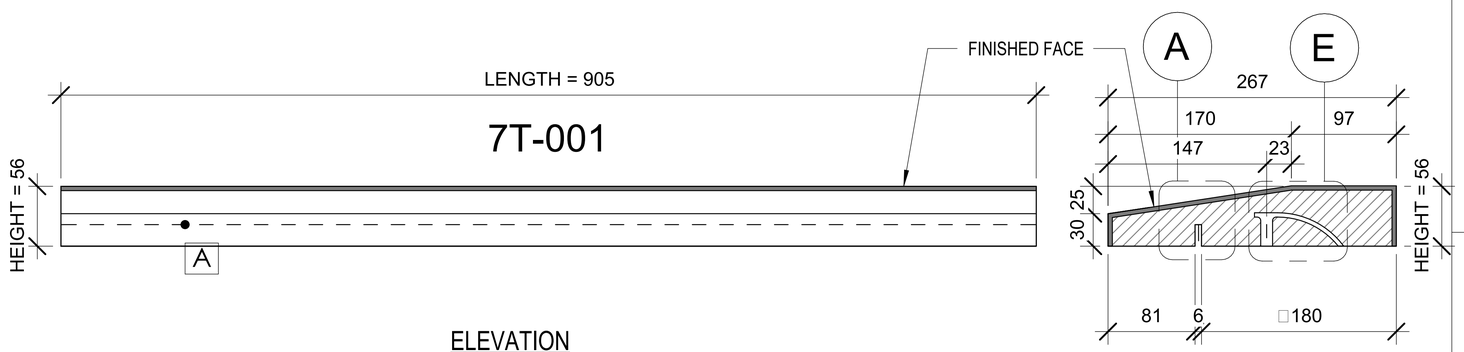
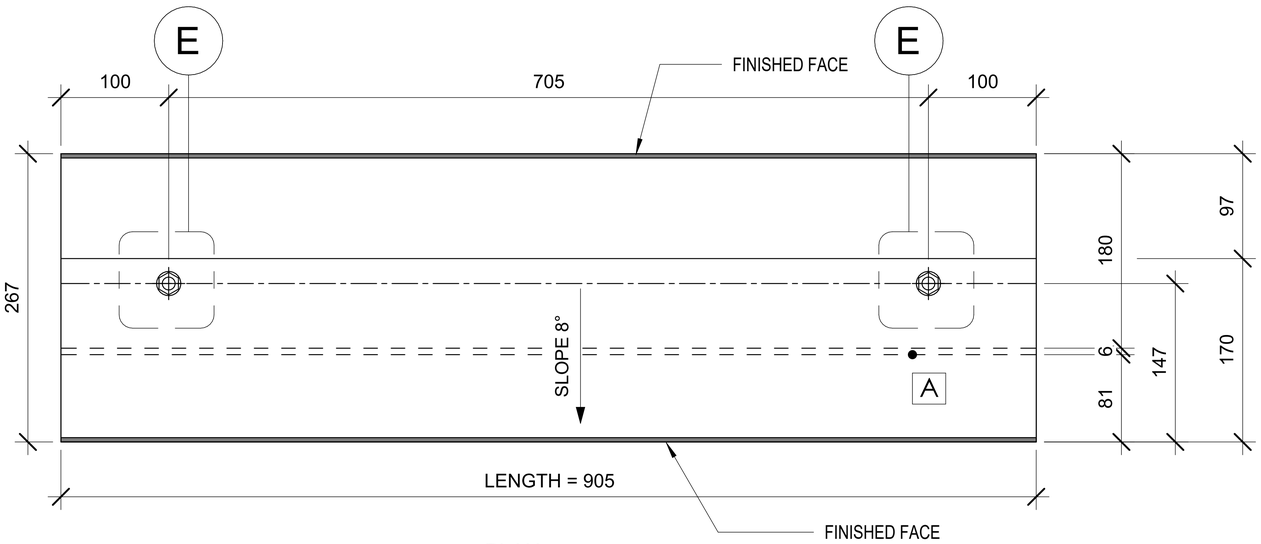
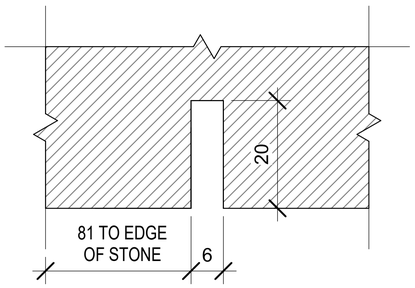
| TICKET NUMBER | LENGTH | HEIGHT | WIDTH | THICKNESS | QUANTITY |
|---|---|---|---|---|---|
| 7T-001 | 905 | 56 | | 267 | |



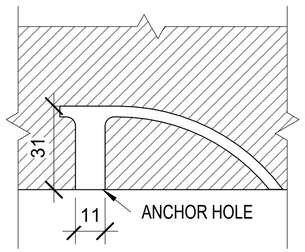

ELEVATION




PLAN




**DETAIL A - KERF (with SSC0 clips)**




**DETAIL E - T-31 ANCHOR HOLE - 3/8" dia x 1¼" deep**

| Rev. | Date | By | Description |
|---|---|---|---|
| 02 | 2025.11.07 | | STONE TICKET PACKAGE P7 For Production |
| 06 | 2025.12.24 | | STONE TICKET PACKAGE P1-P4 and P7 For Production |

| | | | |
|---|---|---|---|
| **TOLERANCE:** | | INHABIT GROUP | |
| **PROJECT No:** | 0001 | http://www.inhabitgroup.com | |
| **CLIENT:** | ECLAD | © Copyright | |
| **DRAWN BY:** | Dararat P. | **CHECKED BY:** | Dararat P. |
| **SCALE:** | Not To Scale | **DATE:** | 24/12/25 |

| | | | |
|---|---|---|---|
| **MATERIAL:** | Blanco Cristal | **FINISH:** | Honed |
| **PROJECT:** | VANCOUVER WASHINGTON TEMPLE | | |
| **TICKET NUMBER:** | 7T-001 | **REVISION:** | 01 |