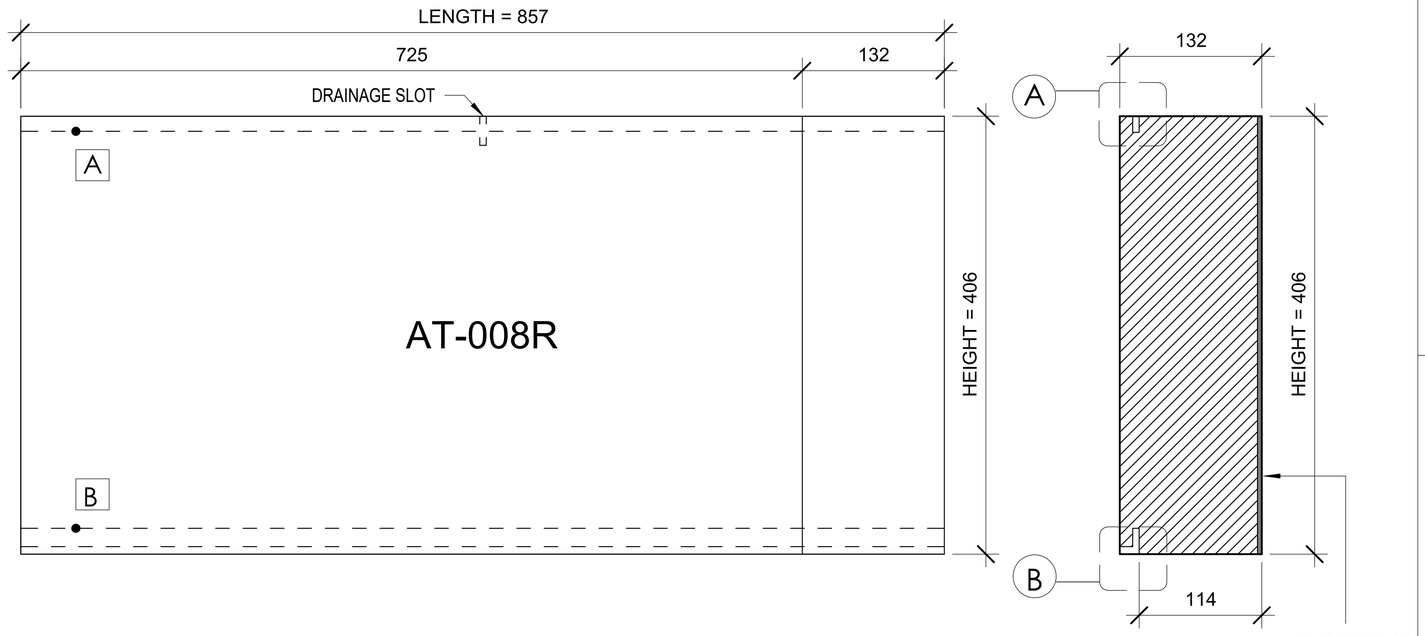
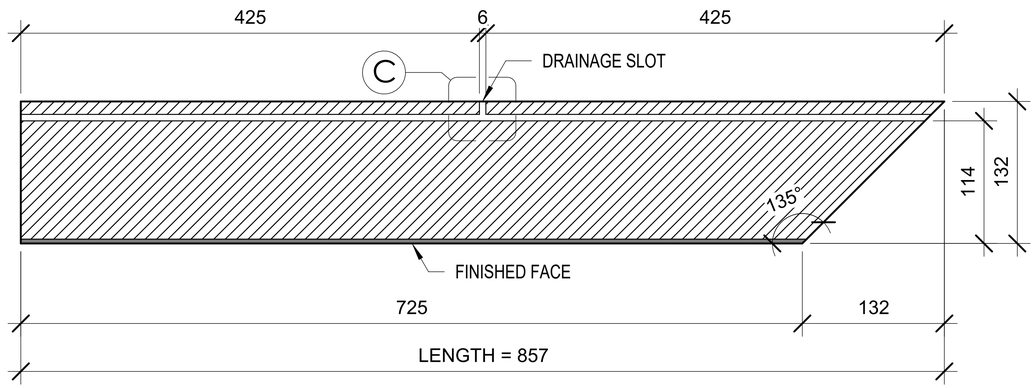
| TICKET NUMBER | LENGTH | HEIGHT | WIDTH | THICKNESS | QUANTITY |
|---|---|---|---|---|---|
| AT-008R | 857 | 406 | | 132 | |



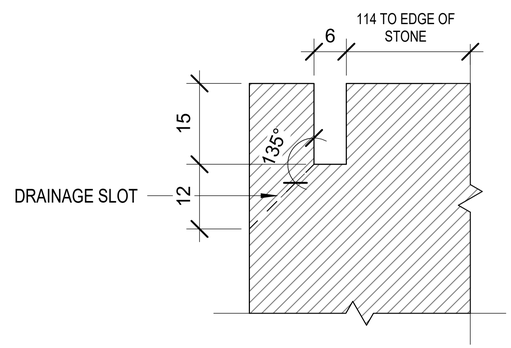

ELEVATION



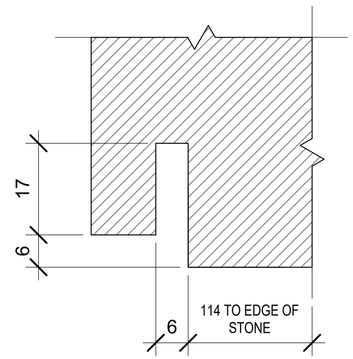

SECTION



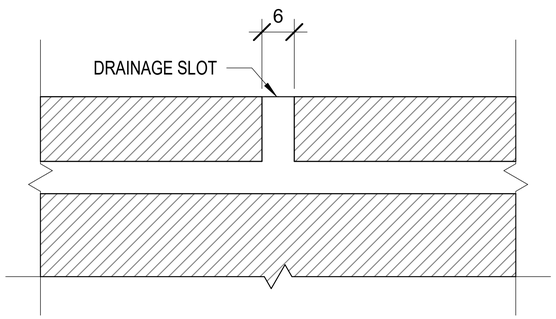

PLAN




**DETAIL A - KERF (thick stone)**




**DETAIL B - REBATED KERF (thick stone)**




**DETAIL C - DRAINAGE SLOT**

| Rev. | Date | By | Description |
|---|---|---|---|
| 00 | 2025.10.02 | - | STONE TICKET PACKAGE P1-P4 For Production |
| 01 | 2025.11.04 | - | STONE TICKET PACKAGE P1-P4 For Production |
| 03 | 2025.11.12 | | STONE TICKET PACKAGE P1-P4 and P7 For Production |
| 06 | 2025.12.24 | | STONE TICKET PACKAGE P1-P4 and P7 For Production |
| | | | |
| | | | |
| | | | |
| | | | |

| | | | |
|---|---|---|---|
| **TOLERANCE:** | | INHABIT GROUP | |
| | | http://www.inhabitgroup.com | |
| | | © Copyright | |
| **PROJECT No:** | 0001 | | |
| **CLIENT:** | ECLAD | | |
| **DRAWN BY:** | Pattarapon P. | **CHECKED BY:** | Dararat P. |
| **SCALE:** | Not To Scale | **DATE:** | 24/12/25 |

| | | | |
|---|---|---|---|
| **MATERIAL:** | Blanco Cristal | **FINISH:** | Honed |
| **PROJECT:** | VANCOUVER WASHINGTON TEMPLE | | |
| **TICKET NUMBER:** | AT-008R | **REVISION:** | 03 |