

TICKET NUMBER	LENGTH	HEIGHT	WIDTH	THICKNESS	QUANTITY
BC-033	1108	371	328	132	


STL FILE TO BE PROVIDED BY ARCHITECT TO FABRICATOR FOR CARVING DETAILS.
Refer to 3D model STL file no.BT-BC-033

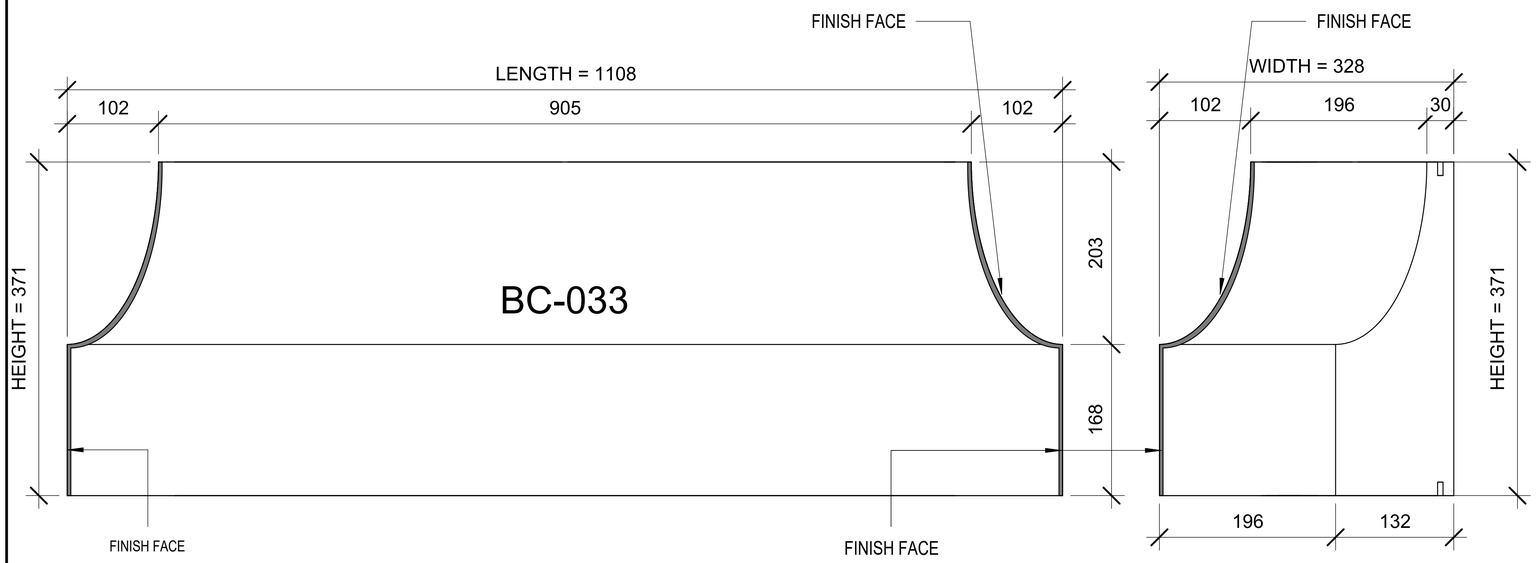

ELEVATION

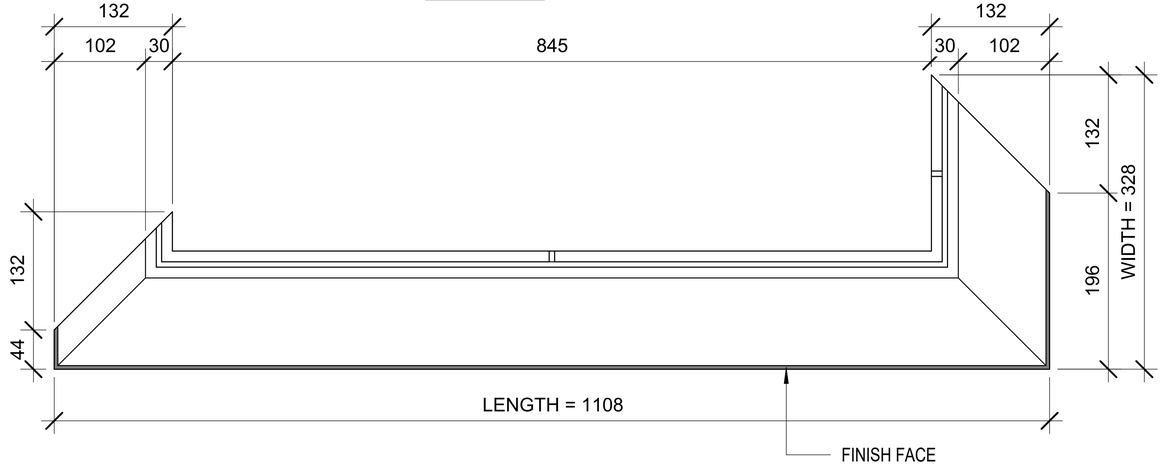

PLAN

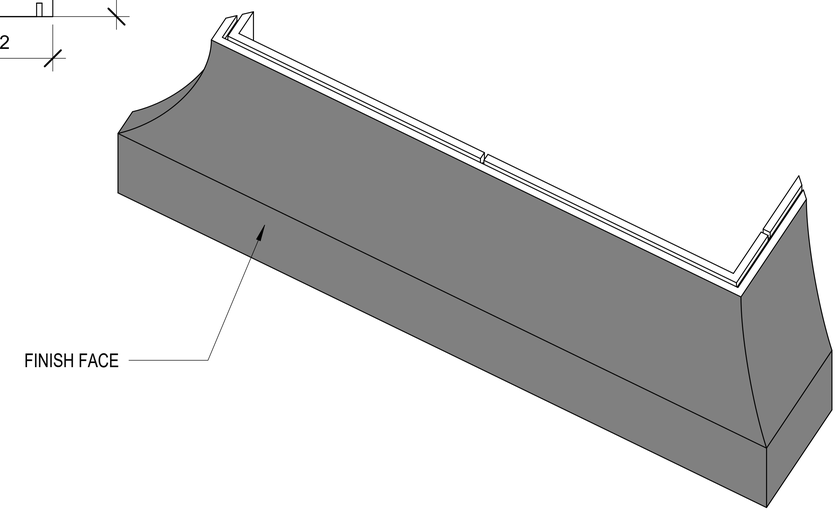

3D MODEL

Rev.	Date	By	Description
09	2026.04.10		STONE TICKET PACKAGE P5, P6 and P8 For Production

TOLERANCE:		INHABIT GROUP	
PROJECT No:	0001	http://www.inhabitgroup.com	
CLIENT:	ECLAD	© Copyright	
DRAWN BY:	Natthapol K.	CHECKED BY:	Dararat P.
SCALE:	Not To Scale	DATE:	10/04/26

MATERIAL:	Blanco Cristal	FINISH:	Honed
PROJECT:	VANCOUVER WASHINGTON TEMPLE		
TICKET NUMBER:	BC-033	REVISION:	00