

TICKET NUMBER	LENGTH	HEIGHT	WIDTH	THICKNESS	QUANTITY
CC-084R	725	448		195	

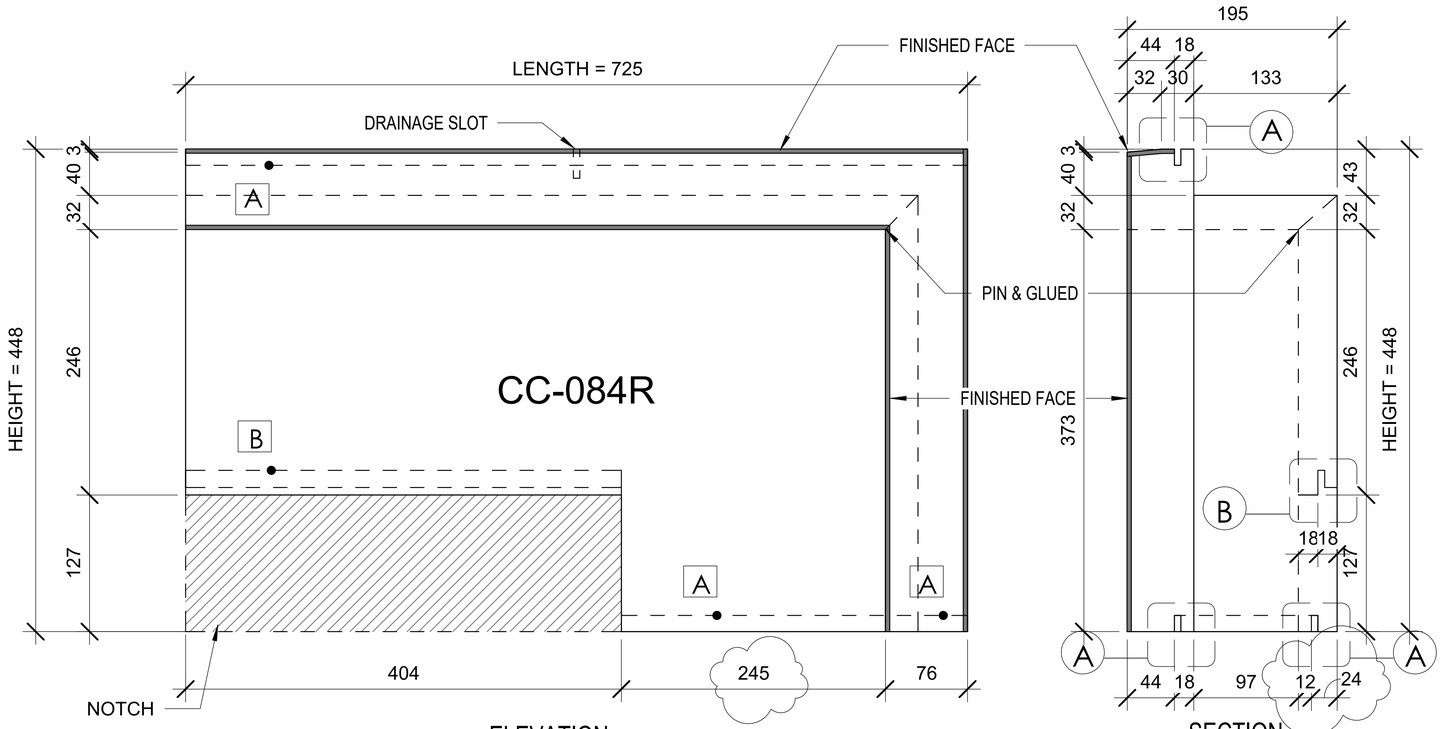


ELEVATION


SECTION

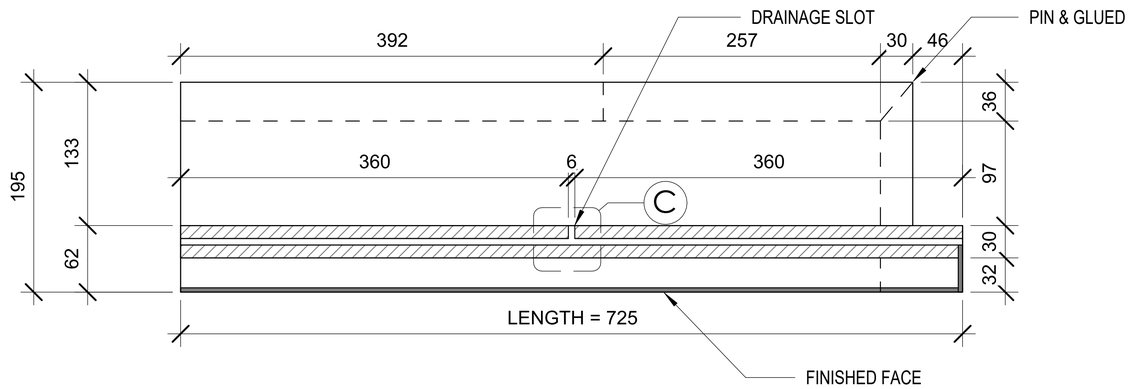


PLAN

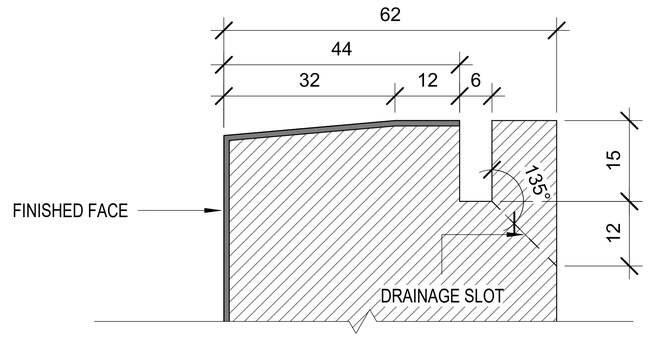


DEL A - KERF (Special-thick stone)

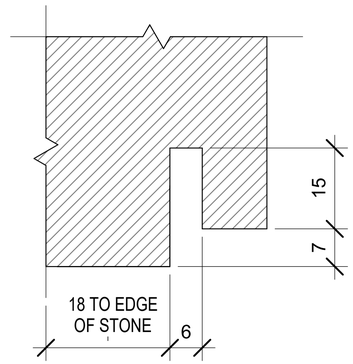


DETAIL B - REBATED KERF (thick stone)

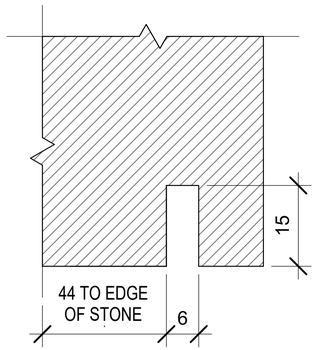

DETAIL A - KERF (thick stone)

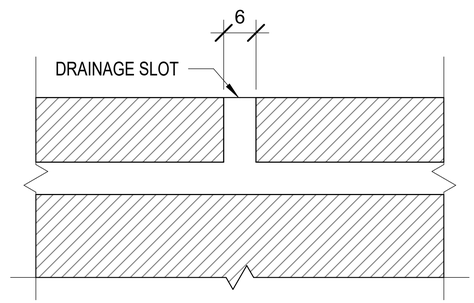

DETAIL C - DRAINAGE SLOT

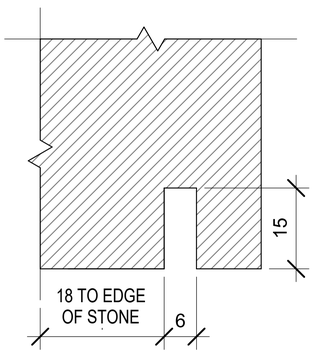

DETAIL A - KERF (thick stone)

Rev.	Date	By	Description
02	2025.11.07		STONE TICKET PACKAGE P7 For Production
03	2025.11.12		STONE TICKET PACKAGE P1-P4 and P7 For Production
06	2025.12.24		STONE TICKET PACKAGE P1-P4 and P7 For Production
08	2026.02.27		STONE TICKET PACKAGE P1-P7 For Production
14	2026.06.26		STONE TICKET PACKAGE P7 and P8 For Production
16	2026.07.08		STONE TICKET PACKAGE P7 For Production

TOLERANCE:		INHABIT GROUP	
		http://www.inhabitgroup.com	
		© Copyright	
PROJECT No:	0001		
CLIENT:	ECLAD		
DRAWN BY:	Dararat P.	**CHECKED BY:**	Dararat P.
SCALE:	Not To Scale	**DATE:**	08/07/26

MATERIAL:	Blanco Cristal	**FINISH:**	Honed
PROJECT:	VANCOUVER WASHINGTON TEMPLE		
TICKET NUMBER:	CC-084R	**REVISION:**	05