

TICKET NUMBER	LENGTH	HEIGHT	WIDTH	THICKNESS	QUANTITY
CC-110R	738	496	194	38	

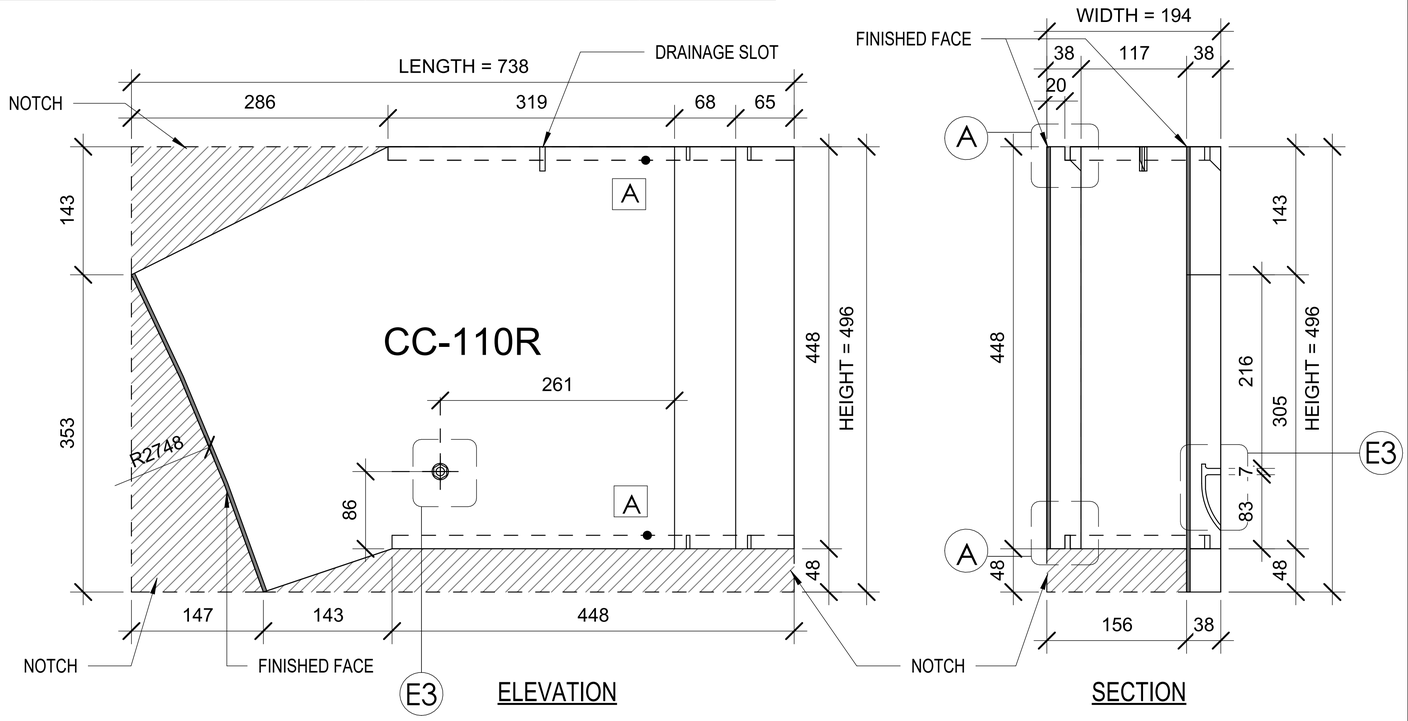


ELEVATION


SECTION

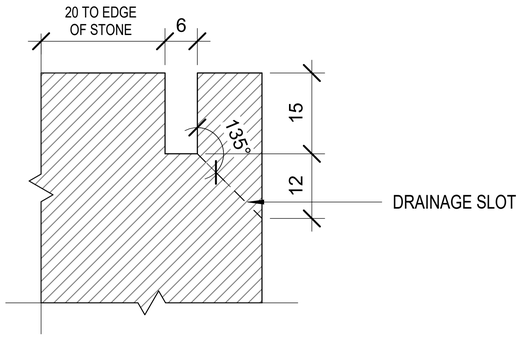


DETAIL A - KERF (thick stone)

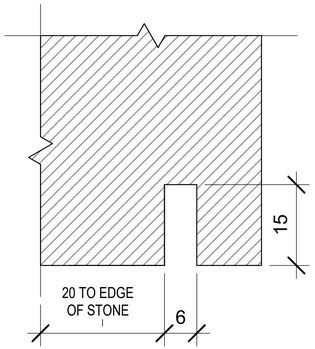


DETAIL A - KERF (thick stone)

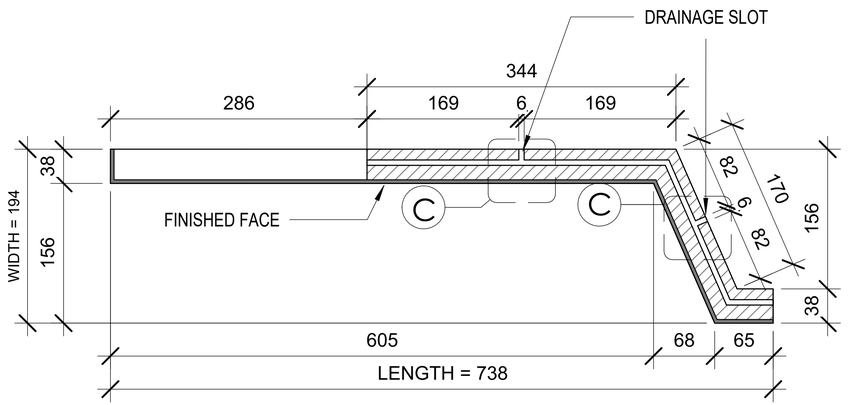

PLAN

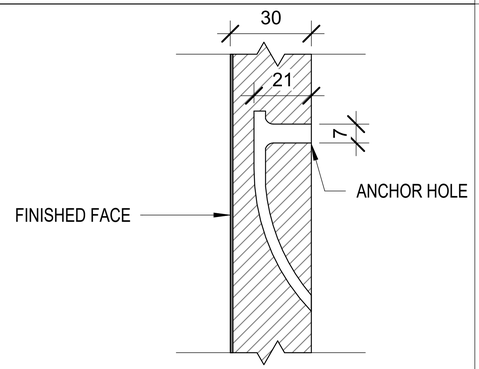

DETAIL E3 - T-31 ANCHOR HOLE (30 mm thick stone) - ¼" dia x ¾" deep

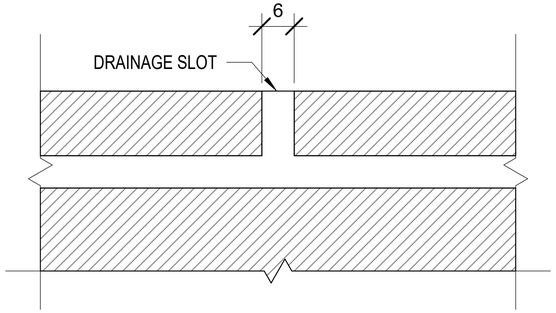

DETAIL C - DRAINAGE SLOT

Rev.	Date	By	Description
04	2025.12.04		STONE TICKET PACKAGE P5 and P7 For Production
07	2026.01.14		STONE TICKET PACKAGE P3, P4, P5 and P6 For Production

TOLERANCE:		INHABIT GROUP	
PROJECT No:	0001	http://www.inhabitgroup.com	
CLIENT:	ECLAD	© Copyright	
DRAWN BY:	Dararat P.	CHECKED BY:	Dararat P.
SCALE:	Not To Scale	DATE:	14/01/26

MATERIAL:	Blanco Cristal	FINISH:	Honed
PROJECT:	VANCOUVER WASHINGTON TEMPLE		
TICKET NUMBER:	CC-110R	REVISION:	01