

TICKET NUMBER	LENGTH	HEIGHT	WIDTH	THICKNESS	QUANTITY
CC-184R	905	448	186	30	

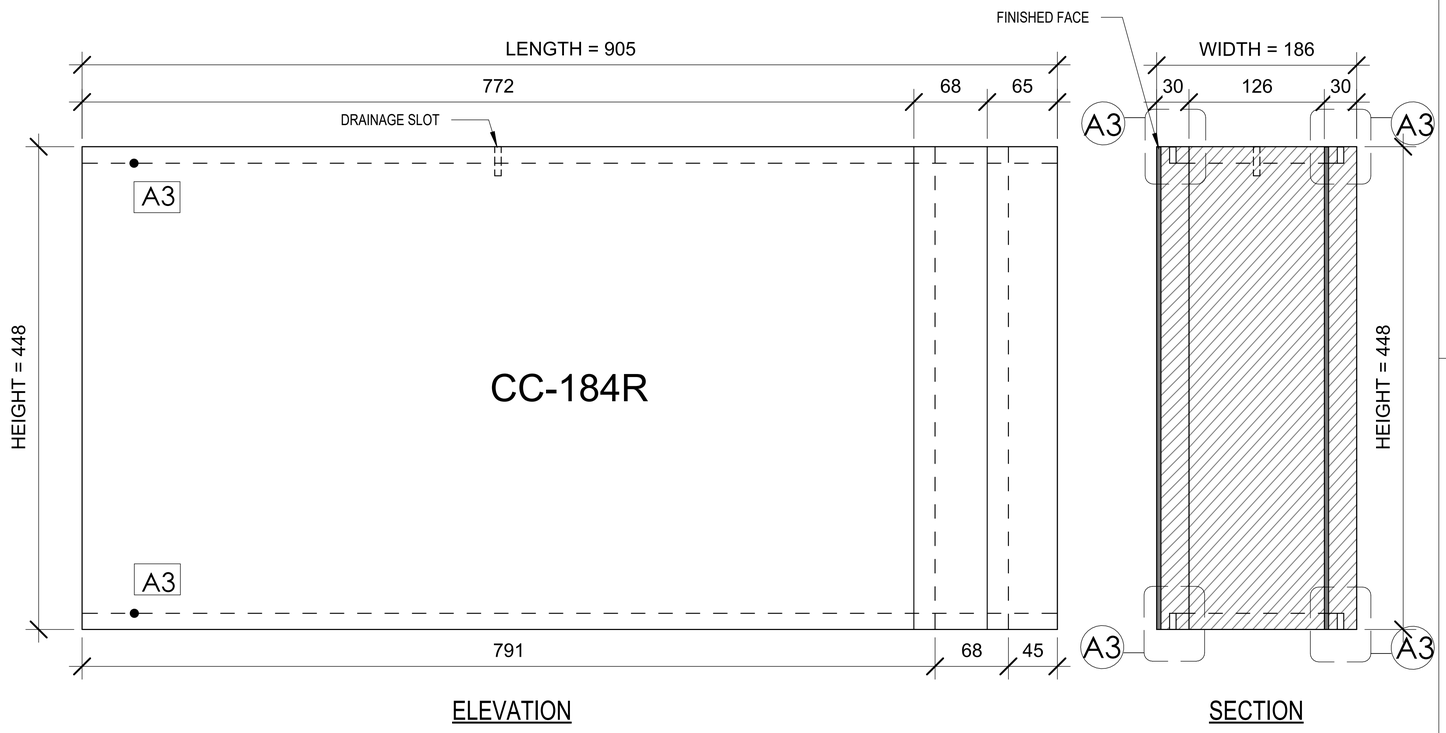


ELEVATION


SECTION

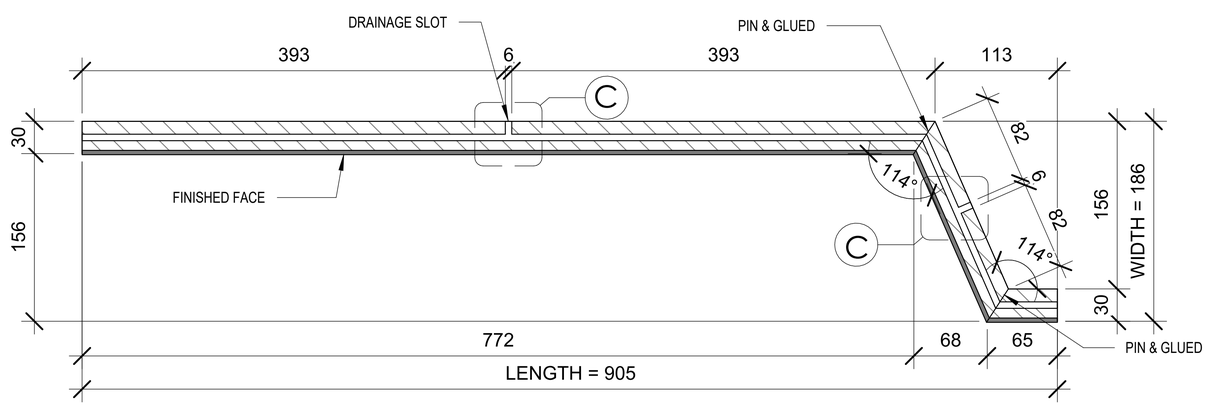


PLAN

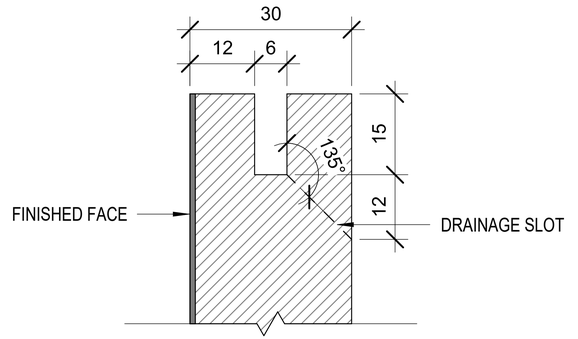

DETAIL A3 - STANDARD KERF (30mm thick stone)

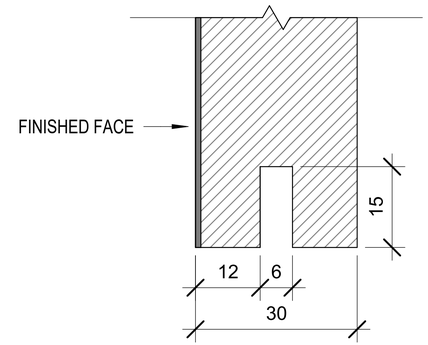

DETAIL A3 - STANDARD KERF (30mm thick stone)

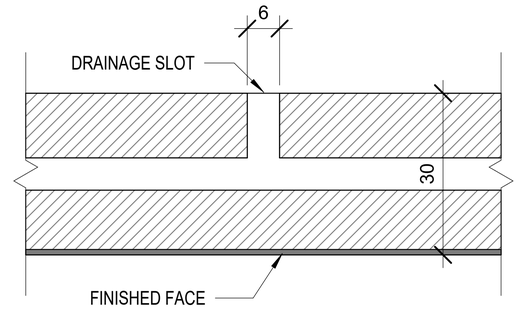

DETAIL C - DRAINAGE SLOT

Rev.	Date	By	Description
05	2025.12.19		STONE TICKET PACKAGE P6 For Production
15	2026.07.02		STONE TICKET PACKAGE P6 For Production

TOLERANCE:		INHABIT GROUP	
		http://www.inhabitgroup.com	
		© Copyright	
PROJECT No:	0001		
CLIENT:	ECLAD		
DRAWN BY:	Natthapol K.	**CHECKED BY:**	Dararat P.
SCALE:	Not To Scale	**DATE:**	02/07/26

MATERIAL:	Blanco Cristal	**FINISH:**	Honed
PROJECT:	VANCOUVER WASHINGTON TEMPLE		
TICKET NUMBER:	CC-184R	**REVISION:**	01