

TICKET NUMBER	LENGTH	HEIGHT	WIDTH	THICKNESS	QUANTITY
CT-051R	946	448		30	

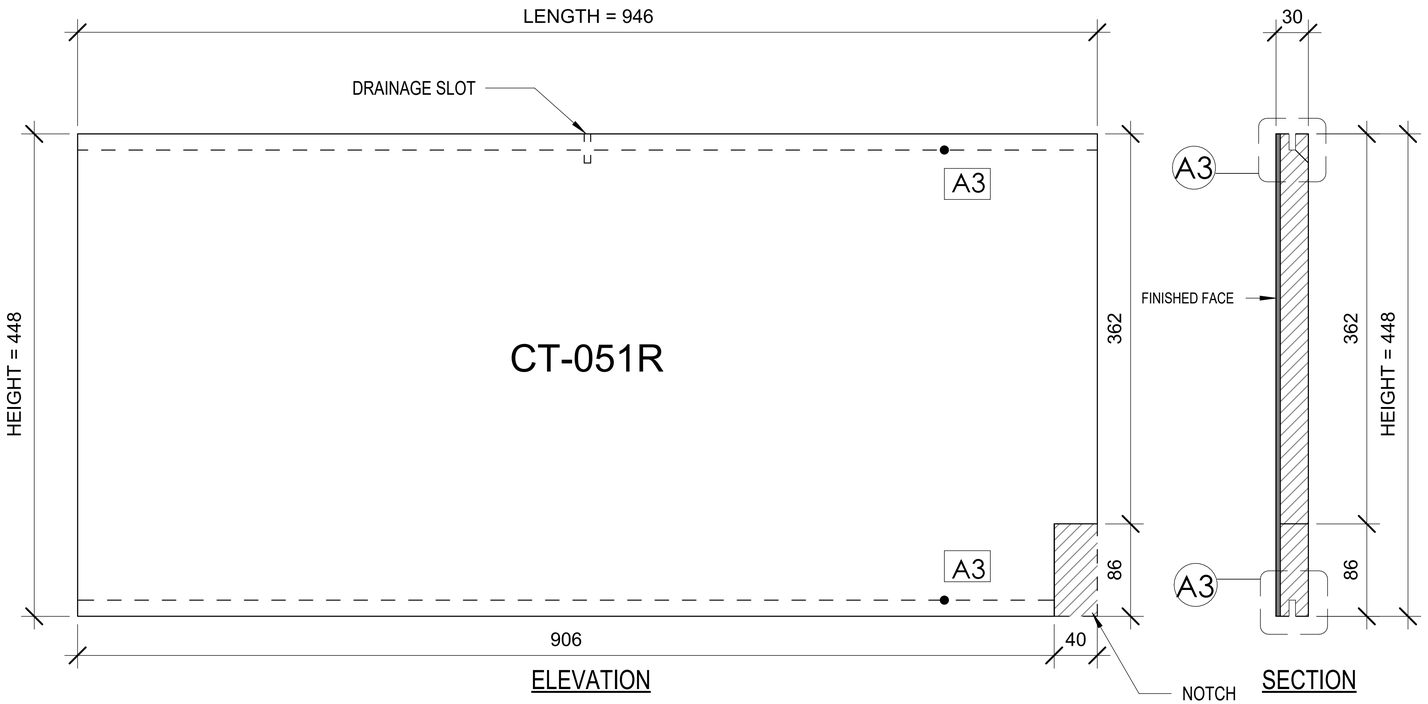


ELEVATION


SECTION

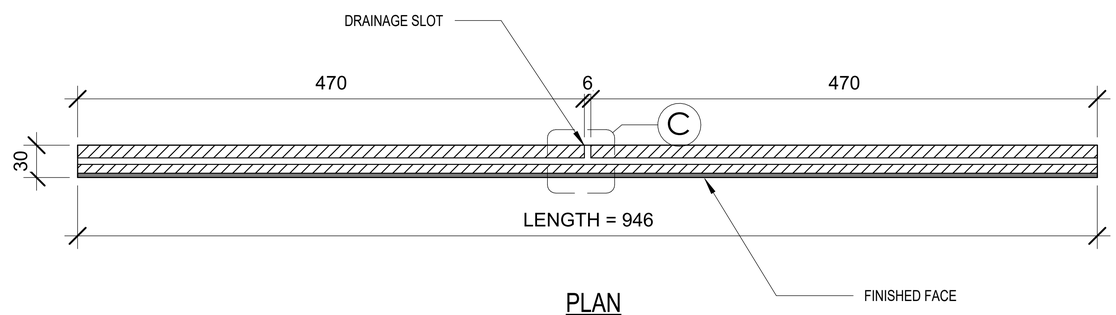


PLAN

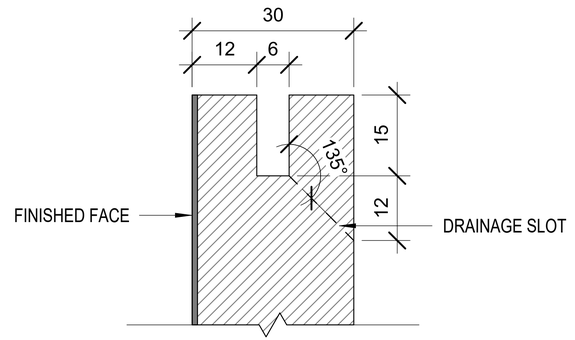

DETAIL A3 - STANDARD KERF (30mm thick stone)

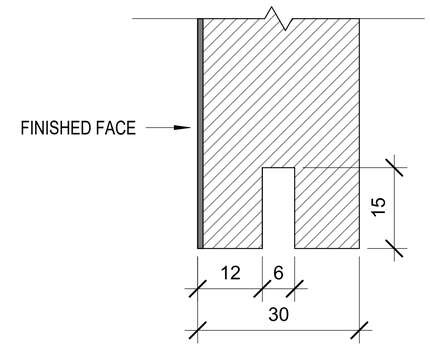

DETAIL A3 - STANDARD KERF (30mm thick stone)

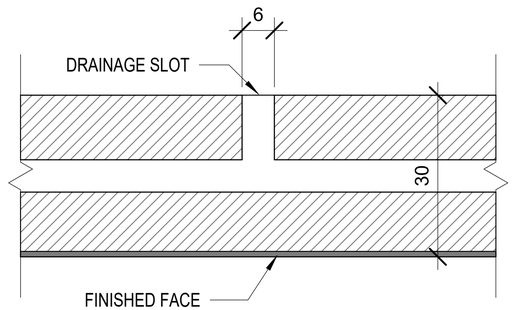

DETAIL C - DRAINAGE SLOT

Rev.	Date	By	Description
00	2025.10.02	-	STONE TICKET PACKAGE P1-P4 For Production
01	2025.11.04	-	STONE TICKET PACKAGE P1-P4 For Production
03	2025.11.12		STONE TICKET PACKAGE P1-P4 and P7 For Production
06	2025.12.24		STONE TICKET PACKAGE P1-P4 and P7 For Production

TOLERANCE:		INHABIT GROUP	
		http://www.inhabitgroup.com	
		© Copyright	
PROJECT No:	0001		
CLIENT:	ECLAD		
DRAWN BY:	Dararat P.	**CHECKED BY:**	Dararat P.
SCALE:	Not To Scale	**DATE:**	24/12/25

MATERIAL:	Blanco Cristal	**FINISH:**	Honed
PROJECT:	VANCOUVER WASHINGTON TEMPLE		
TICKET NUMBER:	CT-051R	**REVISION:**	03