

TICKET NUMBER	LENGTH	HEIGHT	WIDTH	THICKNESS	QUANTITY
CT-190R	1068	380	0	38	

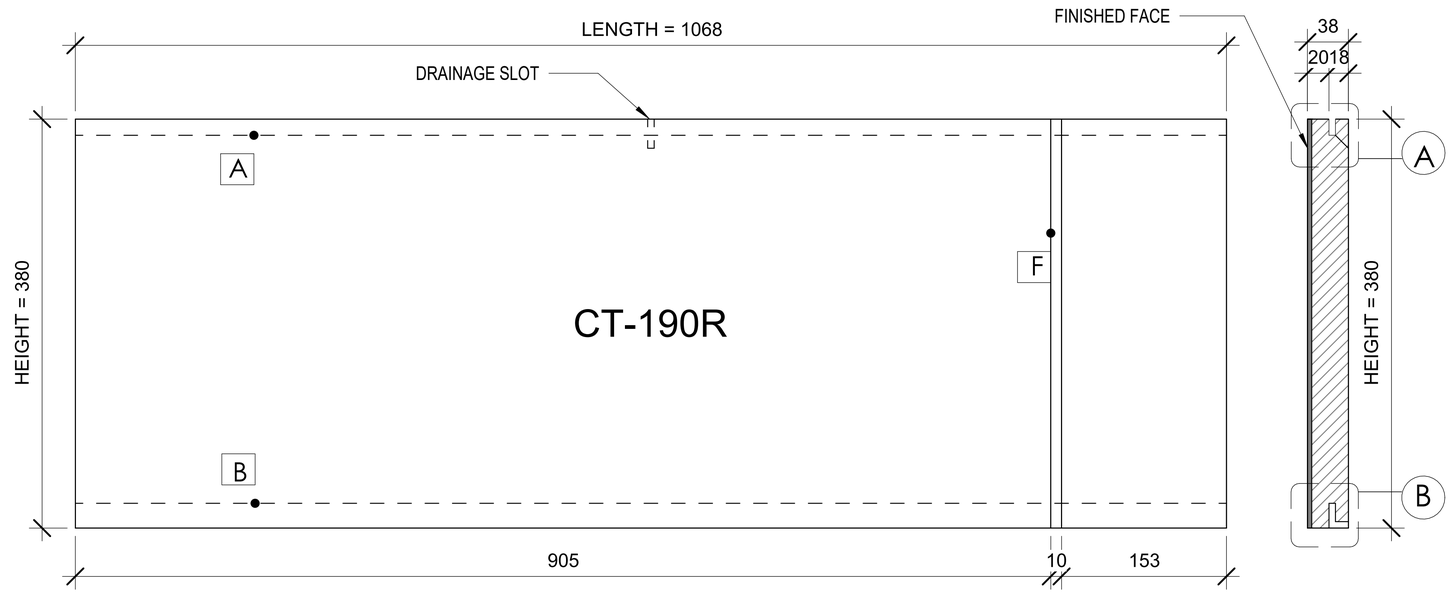


ELEVATION


SECTION

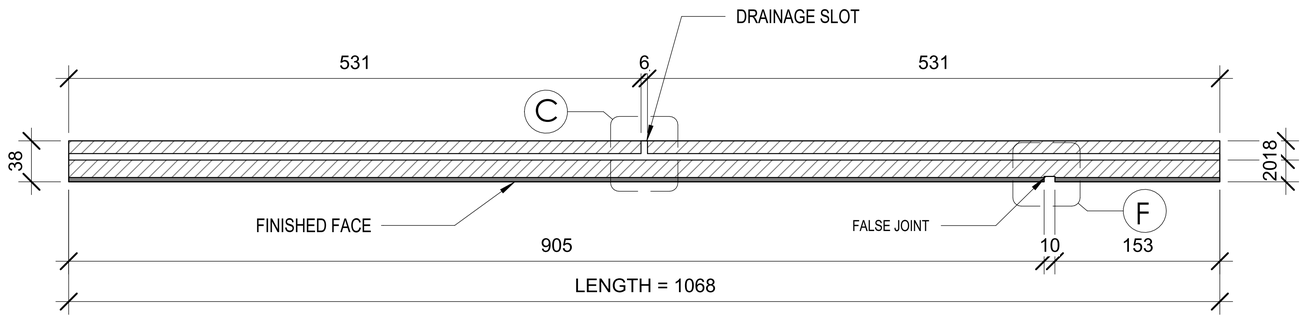


PLAN

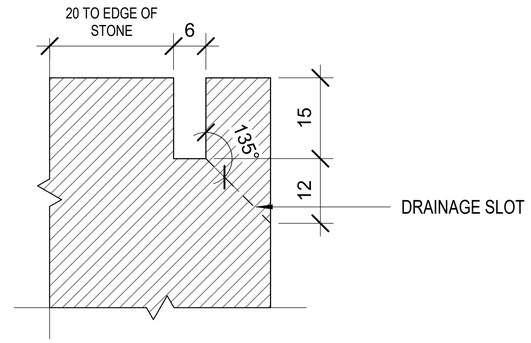


DETAIL A - KERF (thick stone)

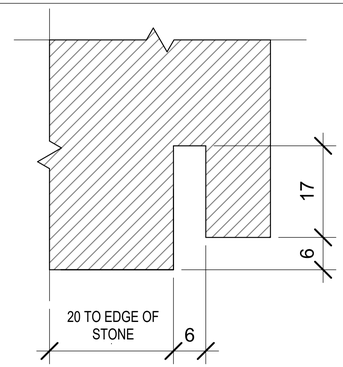

DETAIL B - REBATED KERF (thick stone)

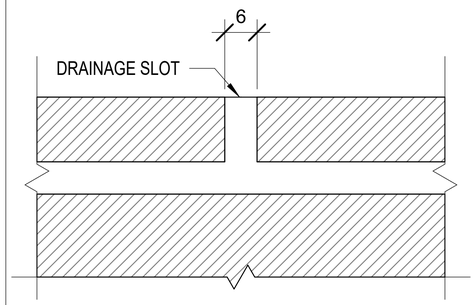

DETAIL C - DRAINAGE SLOT

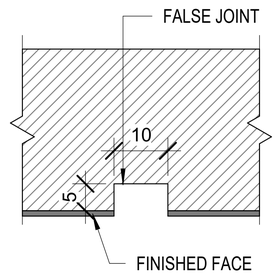

DETAIL F - FALSE JOINT

Rev.	Date	By	Description
09	2026.04.10		STONE TICKET PACKAGE P5, P6 and P8 For Production

TOLERANCE:		INHABIT GROUP	
PROJECT No:	0001	http://www.inhabitgroup.com	
CLIENT:	ECLAD	© Copyright	
DRAWN BY:	Natthapol K.	**CHECKED BY:**	Dararat P.
SCALE:	Not To Scale	**DATE:**	10/04/26

MATERIAL:	Blanco Cristal	**FINISH:**	Honed
PROJECT:	VANCOUVER WASHINGTON TEMPLE		
TICKET NUMBER:	CT-190R	**REVISION:**	00