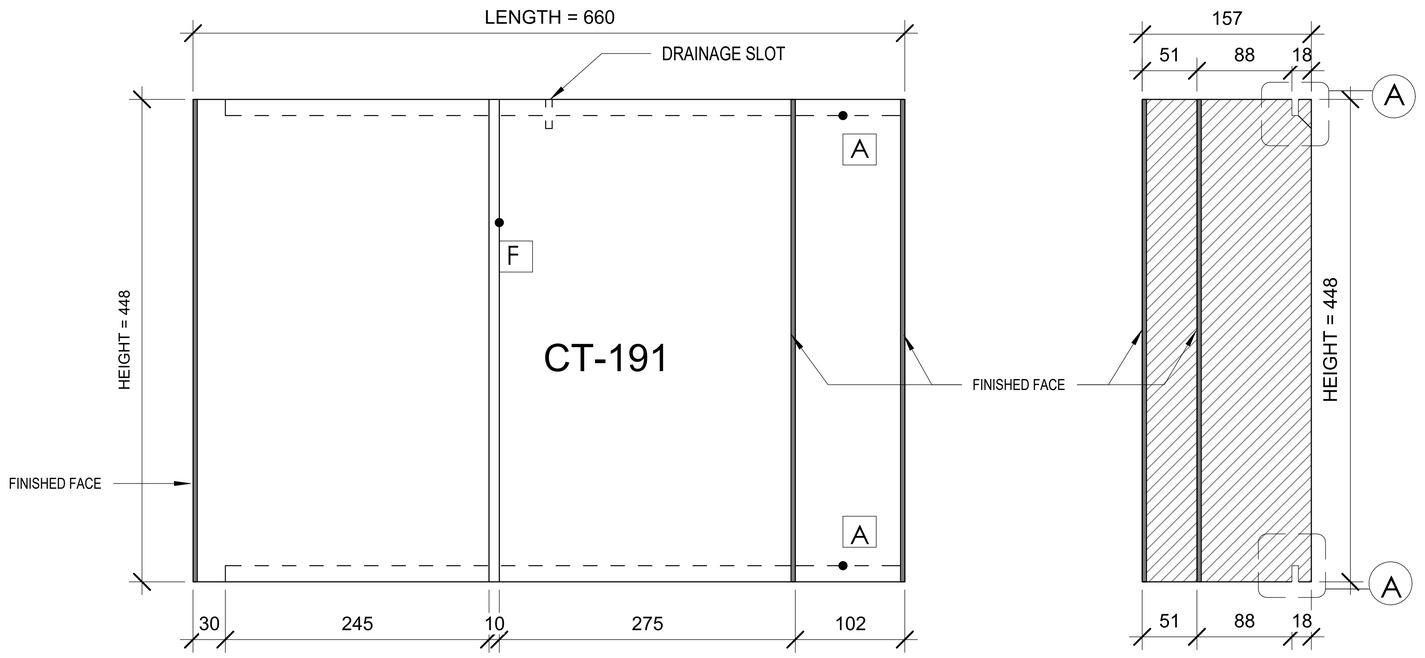
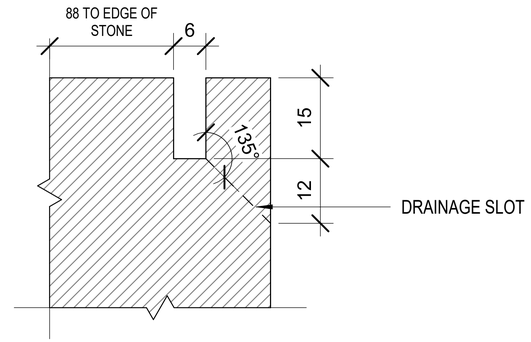
| TICKET NUMBER | LENGTH | HEIGHT | WIDTH | THICKNESS | QUANTITY |
|---|---|---|---|---|---|
| CT-191 | 660 | 448 | 0 | 157 | |



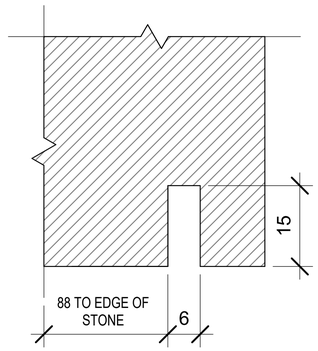

ELEVATION



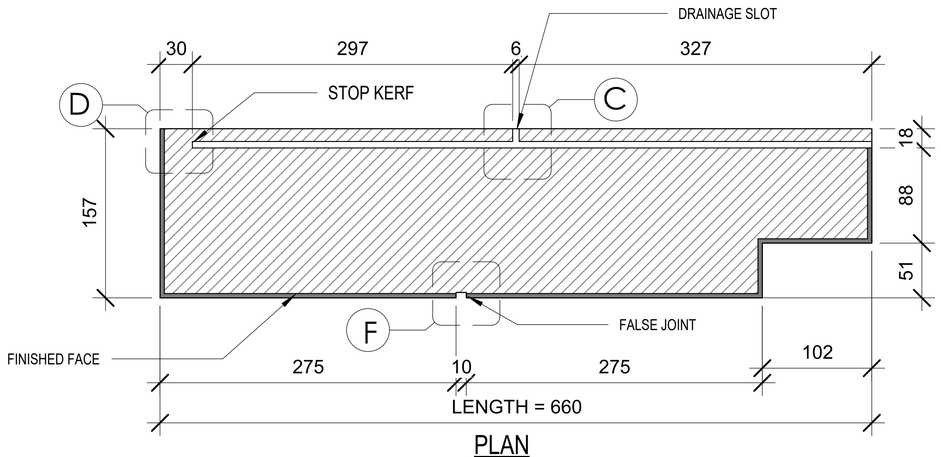

SECTION



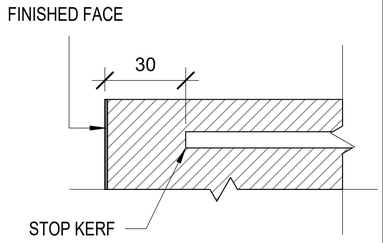

**DETAIL A - KERF (thick stone)**



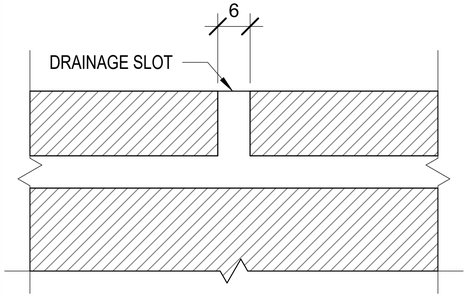

**DETAIL A - KERF (thick stone)**



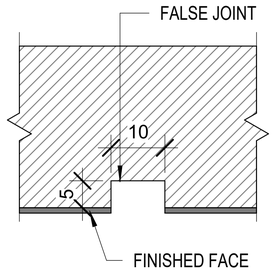

PLAN




**DETAIL D - STOP KERF**




**DETAIL C - DRAINAGE SLOT**




**DETAIL F - FALSE JOINT**

| Rev. | Date | By | Description |
|---|---|---|---|
| 09 | 2026.04.10 | | STONE TICKET PACKAGE P5, P6 and P8 For Production |

| | | | |
|---|---|---|---|
| **TOLERANCE:** | | INHABIT GROUP | |
| | | http://www.inhabitgroup.com | |
| | | © Copyright | |
| **PROJECT No:** | 0001 | | |
| **CLIENT:** | ECLAD | | |
| **DRAWN BY:** | Natthapol K. | **CHECKED BY:** | Dararat P. |
| **SCALE:** | Not To Scale | **DATE:** | 10/04/26 |

| | | | |
|---|---|---|---|
| **MATERIAL:** | Blanco Cristal | **FINISH:** | Honed |
| **PROJECT:** | VANCOUVER WASHINGTON TEMPLE | | |
| **TICKET NUMBER:** | CT-191 | **REVISION:** | 00 |