

TICKET NUMBER	LENGTH	HEIGHT	WIDTH	THICKNESS	QUANTITY
CT-201	565	448	0	146	

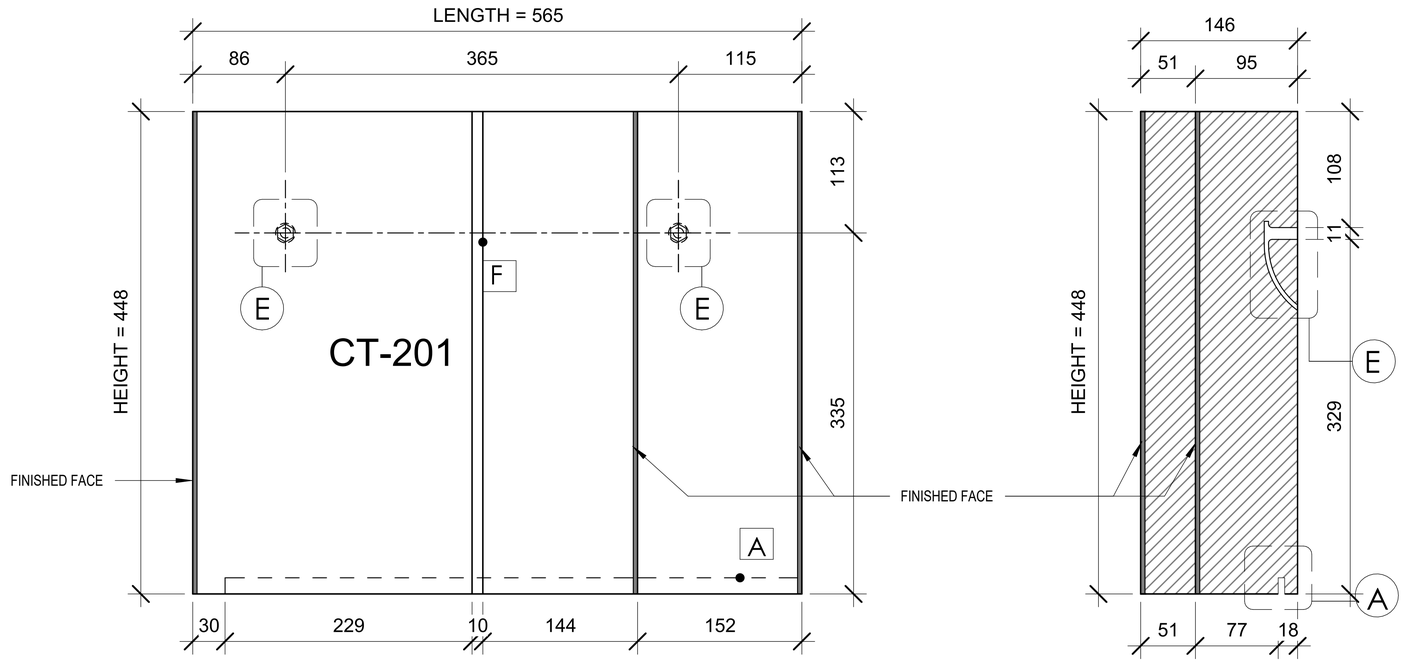


ELEVATION


SECTION

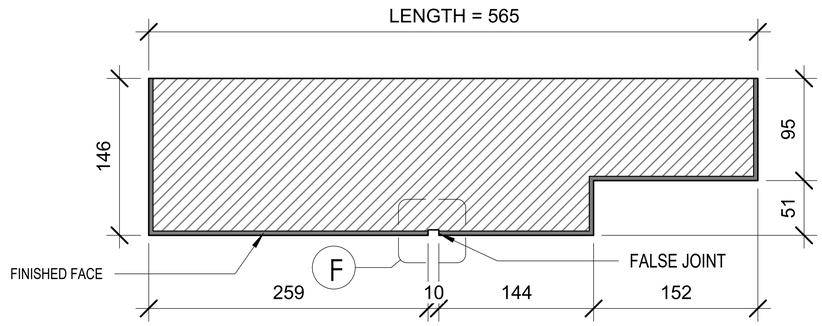


PLAN

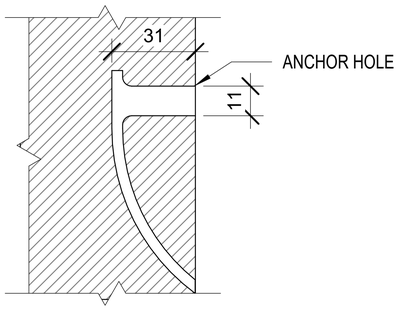

DETAIL E - T-31 ANCHOR HOLE - 3/8" dia x 1¼" deep

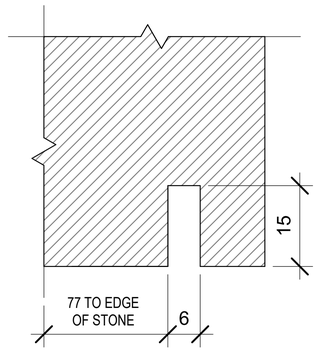

DETAIL A - KERF (thick stone)

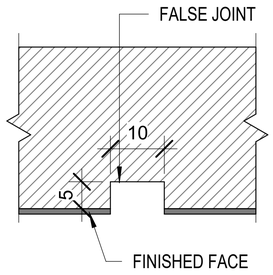

DETAIL F - FALSE JOINT

Rev.	Date	By	Description
09	2026.04.10		STONE TICKET PACKAGE P5, P6 and P8 For Production
11	2026.05.15		STONE TICKET PACKAGE P3,P4,P7 and P8 For Production

TOLERANCE:		INHABIT GROUP	
		http://www.inhabitgroup.com	
		© Copyright	
PROJECT No:	0001		
CLIENT:	ECLAD		
DRAWN BY:	Natthapol K.	**CHECKED BY:**	Dararat P.
SCALE:	Not To Scale	**DATE:**	15/05/26

MATERIAL:	Blanco Cristal	**FINISH:**	Honed
PROJECT:	VANCOUVER WASHINGTON TEMPLE		
TICKET NUMBER:	CT-201	**REVISION:**	01