

TICKET NUMBER	LENGTH	HEIGHT	WIDTH	THICKNESS	QUANTITY
DC-028R	916	295		119	


STL FILE TO BE PROVIDED BY ARCHITECT TO FABRICATOR FOR CARVING DETAILS.
Refer to 3D model STL file no.DC-028R

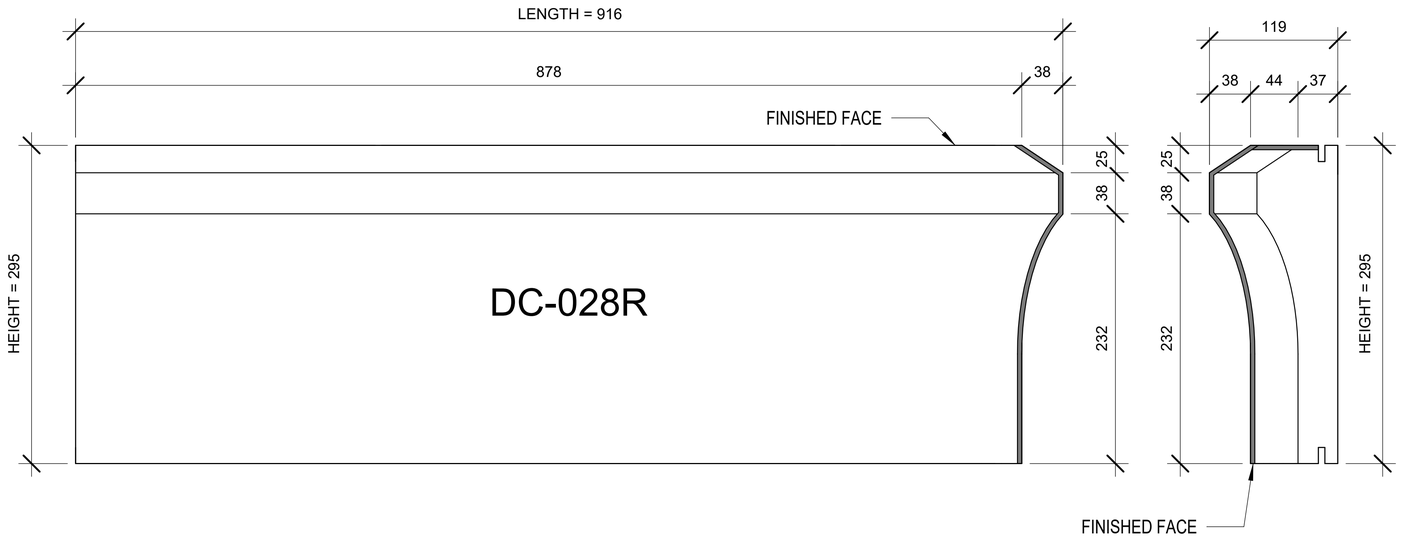

ELEVATION

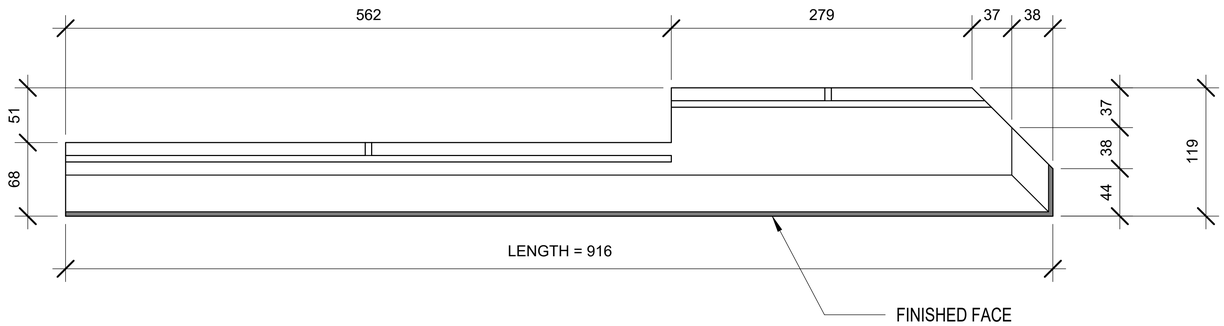

PLAN

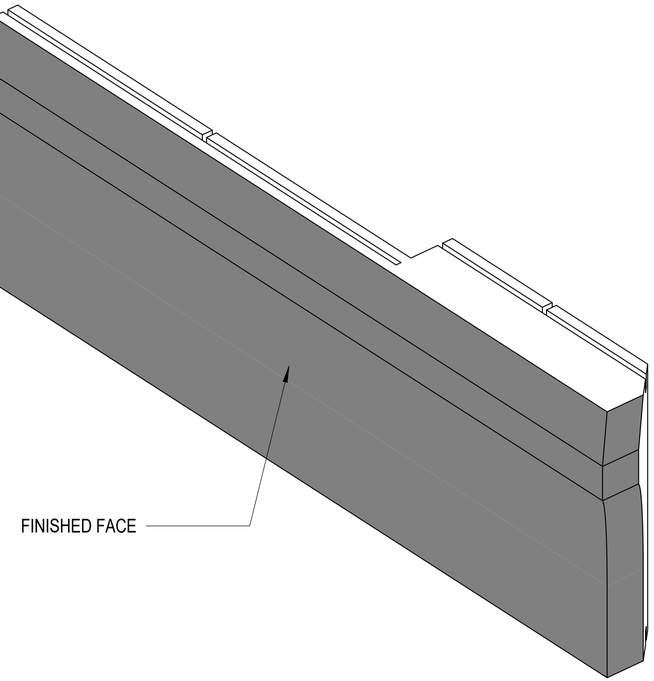

3D MODEL

Rev.	Date	By	Description
04	2025.12.04		STONE TICKET PACKAGE P5 and P7 For Production
07	2026.01.14		STONE TICKET PACKAGE P3, P4, P5 and P6 For Production
09	2026.04.10		STONE TICKET PACKAGE P5, P6 and P8 For Production

TOLERANCE:		INHABIT GROUP	
PROJECT No:	0001	http://www.inhabitgroup.com	
CLIENT:	ECLAD	© Copyright	
DRAWN BY:	Dararat P.	**CHECKED BY:**	Dararat P.
SCALE:	Not To Scale	**DATE:**	10/04/26

MATERIAL:	Blanco Cristal	**FINISH:**	Honed
PROJECT:	VANCOUVER WASHINGTON TEMPLE		
TICKET NUMBER:	DC-028R	**REVISION:**	02