

TICKET NUMBER	LENGTH	HEIGHT	WIDTH	THICKNESS	QUANTITY
FT-008	565	356	0	146	

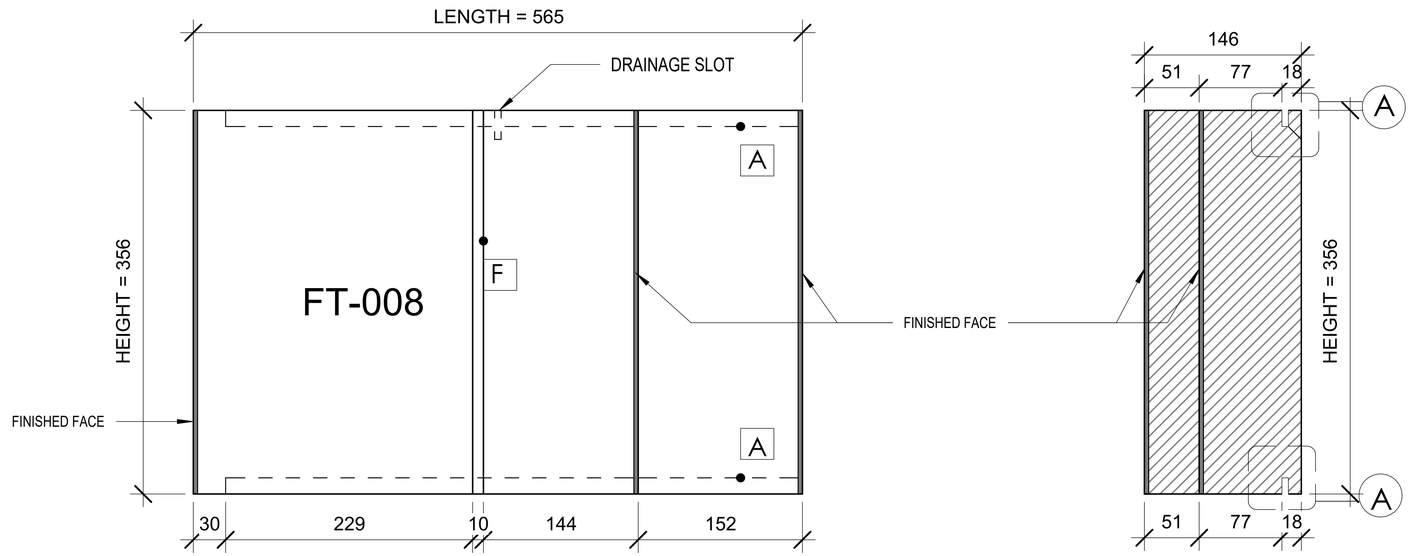


ELEVATION


SECTION

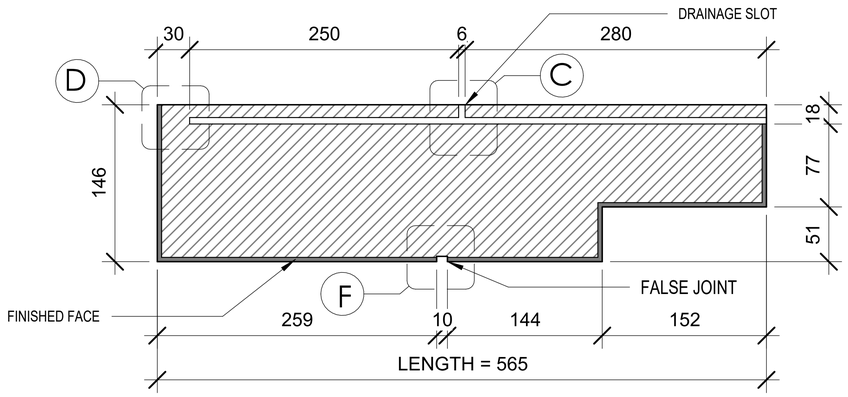


PLAN

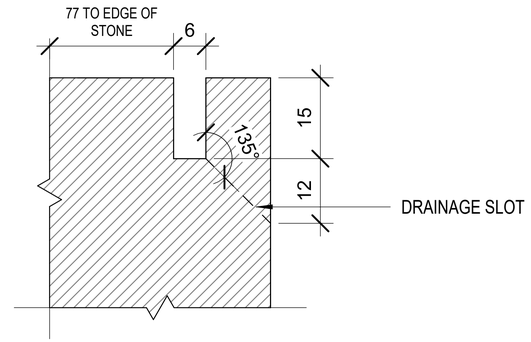


DETAIL A - KERF (thick stone)

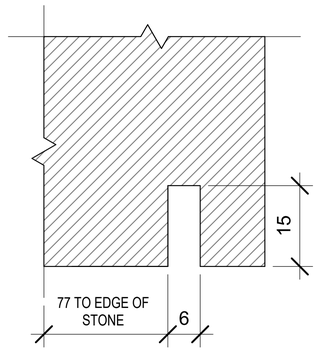


DETAIL A - KERF (thick stone)

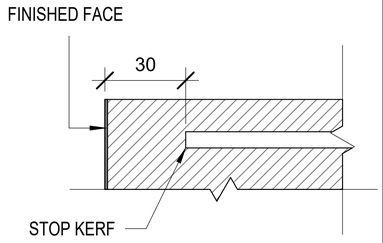

DETAIL D - STOP KERF

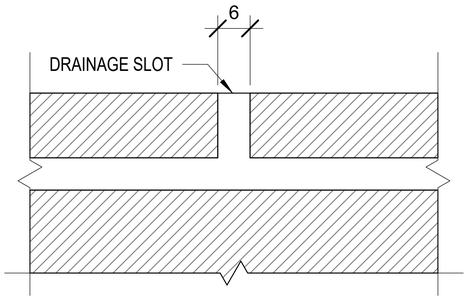

DETAIL C - DRAINAGE SLOT

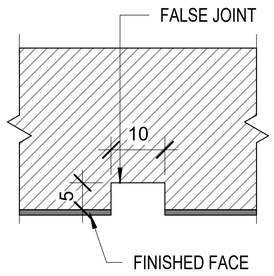

DETAIL F - FALSE JOINT

Rev.	Date	By	Description
09	2026.04.10		STONE TICKET PACKAGE P5, P6 and P8 For Production

TOLERANCE:		INHABIT GROUP	
PROJECT No:	0001	http://www.inhabitgroup.com	
CLIENT:	ECLAD	© Copyright	
DRAWN BY:	Natthapol K.	CHECKED BY:	Dararat P.
SCALE:	Not To Scale	DATE:	10/04/26

MATERIAL: Blanco Cristal

FINISH: Honed

PROJECT: VANCOUVER WASHINGTON TEMPLE

TICKET NUMBER: FT-008

REVISION: 00