


TICKET NUMBER	LENGTH	HEIGHT	WIDTH	THICKNESS	QUANTITY
HC-010	737	58	431	216	

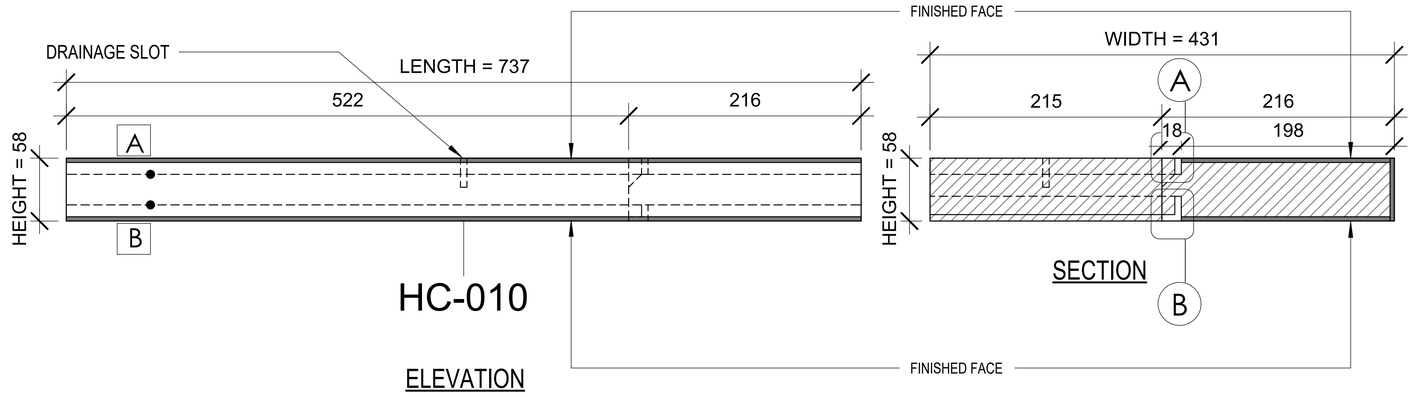


ELEVATION

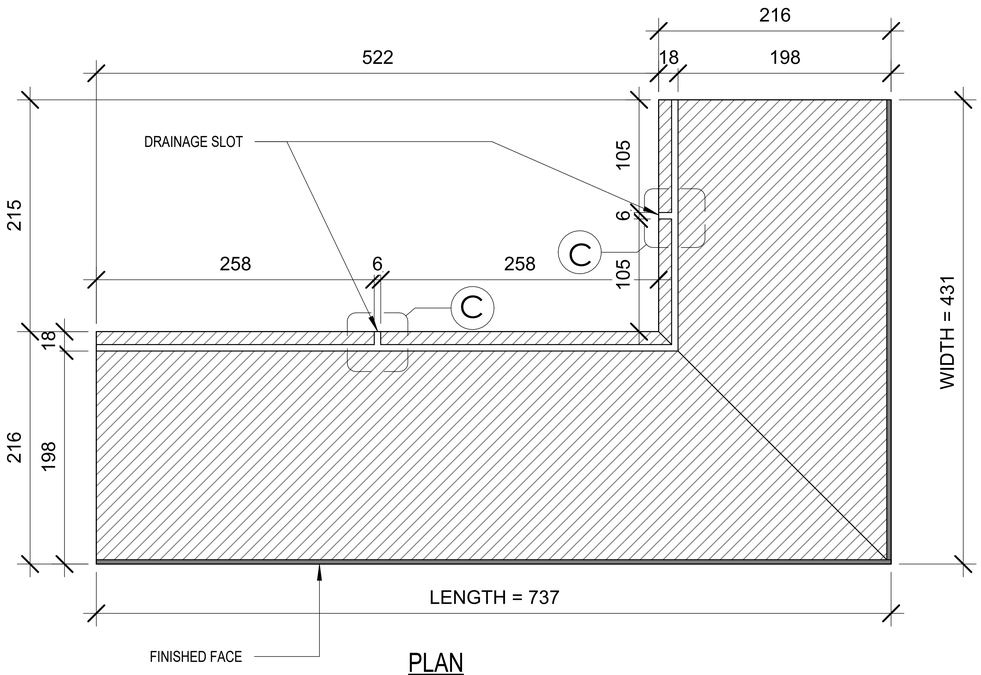


PLAN

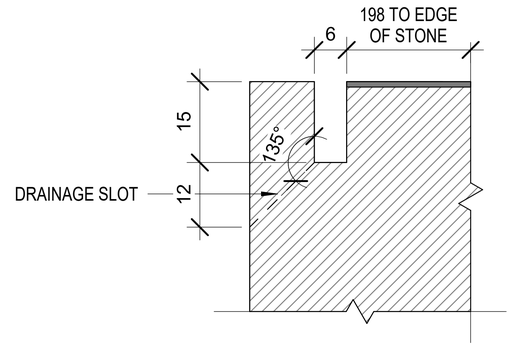

DETAIL A - KERF (thick stone)

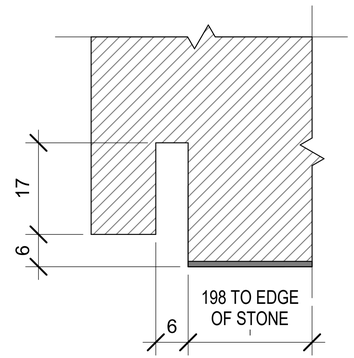

DETAIL B - REBATED KERF (thick stone)

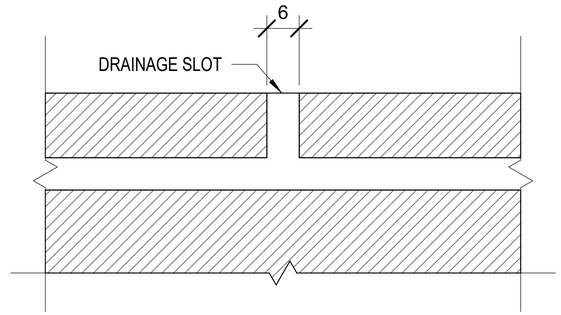

DETAIL C - DRAINAGE SLOT

Rev.	Date	By	Description
10	2026.04.24		STONE TICKET PACKAGE P5 and P8 For Production

TOLERANCE:		INHABIT GROUP	
PROJECT No:	0001	http://www.inhabitgroup.com	
CLIENT:	ECLAD	© Copyright	
DRAWN BY:	Natthapol K.	CHECKED BY:	Dararat P.
SCALE:	Not To Scale	DATE:	24/04/26

MATERIAL:	Blanco Cristal	**FINISH:**	Honed
PROJECT:	VANCOUVER WASHINGTON TEMPLE		
TICKET NUMBER:	HC-010	**REVISION:**	00