

TICKET NUMBER	LENGTH	HEIGHT	WIDTH	THICKNESS	QUANTITY
HT-015	1000	58	0	216	

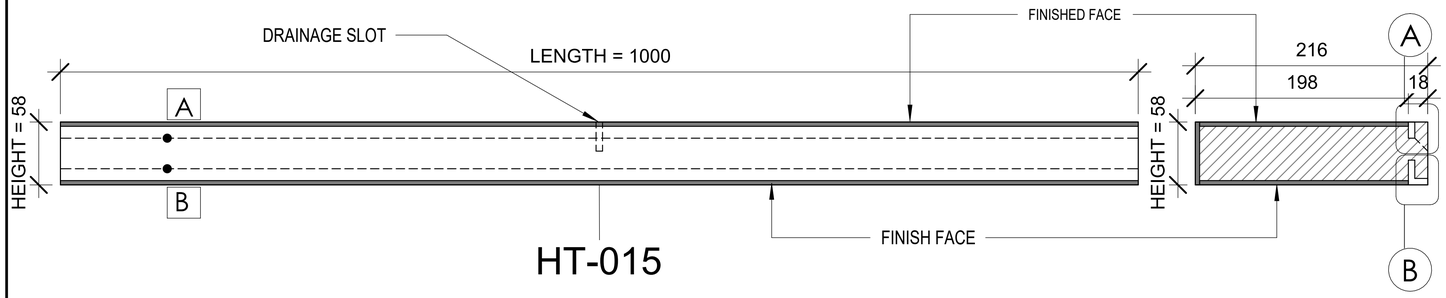


HT-015


ELEVATION SECTION

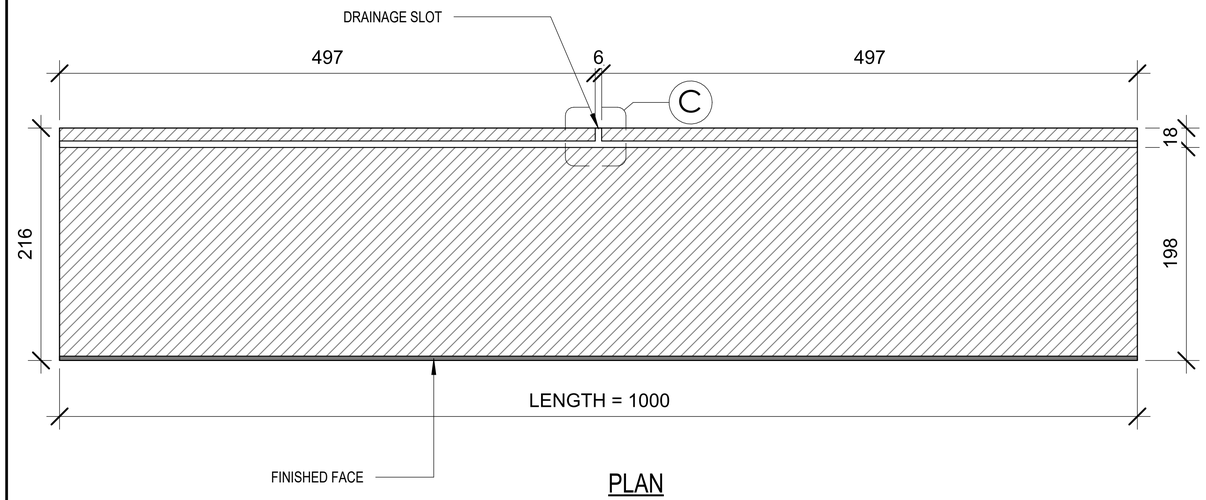


PLAN

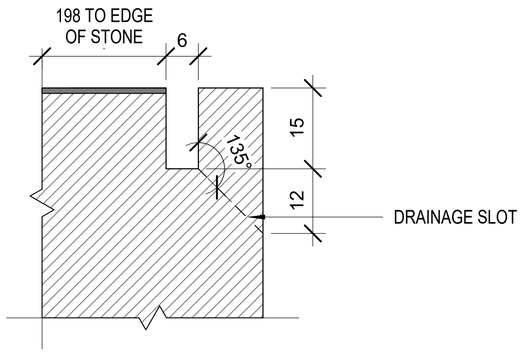

DETAIL A - KERF (thick stone)

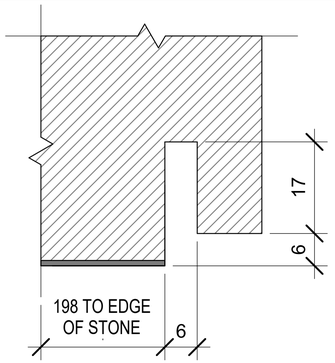

DETAIL B - REBATED KERF (thick stone)

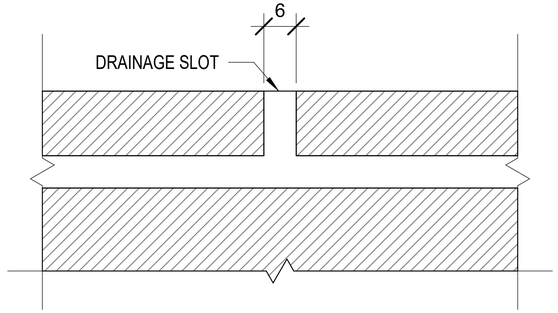

DETAIL C - DRAINAGE SLOT

Rev.	Date	By	Description
10	2026.04.24		STONE TICKET PACKAGE P5 and P8 For Production

TOLERANCE:		INHABIT GROUP	
		http://www.inhabitgroup.com	
		© Copyright	
PROJECT No:	0001		
CLIENT:	ECLAD		
DRAWN BY:	Natthapol K.	CHECKED BY:	Dararat P.
SCALE:	Not To Scale	DATE:	24/04/26

MATERIAL:	Blanco Cristal	FINISH:	Honed
PROJECT:	VANCOUVER WASHINGTON TEMPLE		
TICKET NUMBER:	HT-015	REVISION:	00