

TICKET NUMBER	LENGTH	HEIGHT	WIDTH	THICKNESS	QUANTITY
HT-018R	1068	59	0	487	

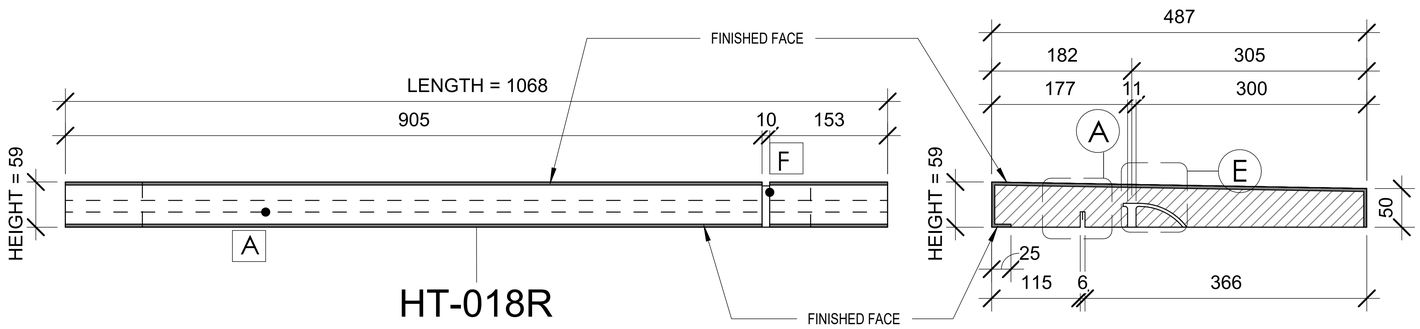


ELEVATION


SECTION

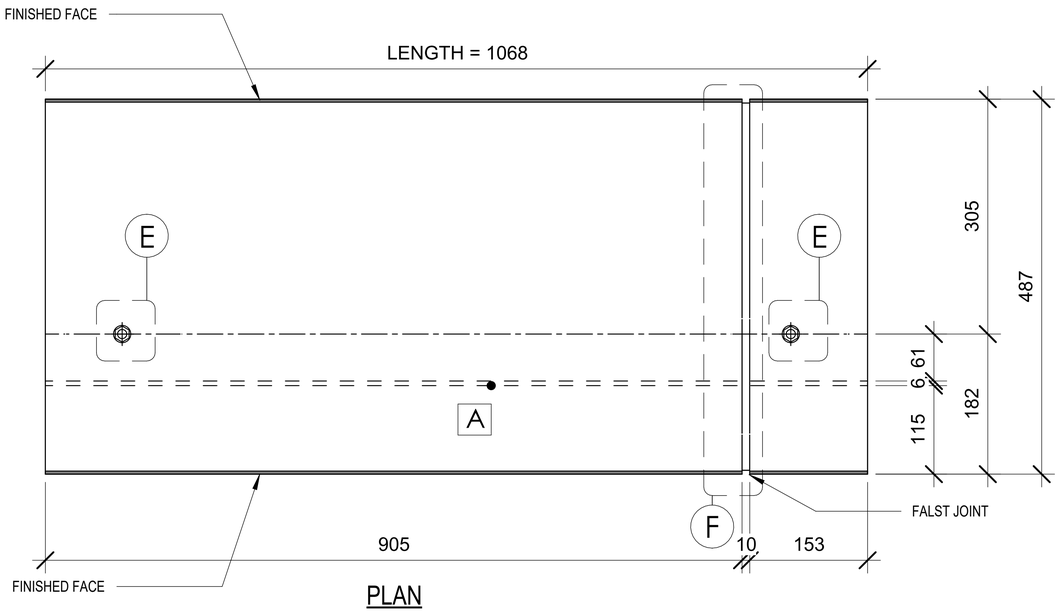


PLAN

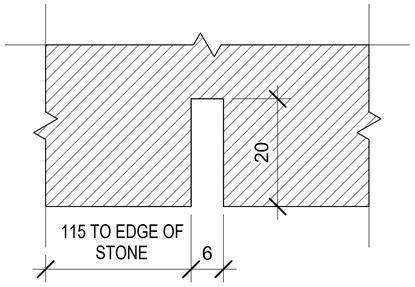

DETAIL A - KERF (with SSC0 clips)

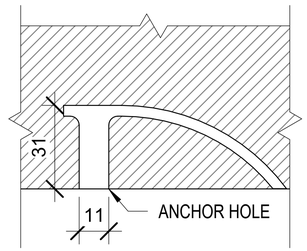

DETAIL E - T-31 ANCHOR HOLE - 3/8" dia x 1¼" deep

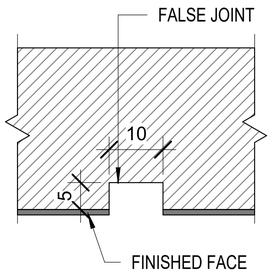

DETAIL F - FALSE JOINT

Rev.	Date	By	Description
10	2026.04.24		STONE TICKET PACKAGE P5 and P8 For Production

TOLERANCE:		INHABIT GROUP	
		http://www.inhabitgroup.com	
		© Copyright	
PROJECT No:	0001		
CLIENT:	ECLAD		
DRAWN BY:	Natthapol K.	CHECKED BY:	Dararat P.
SCALE:	Not To Scale	DATE:	24/04/26

MATERIAL:	Blanco Cristal	FINISH:	Honed
PROJECT:	VANCOUVER WASHINGTON TEMPLE		
TICKET NUMBER:	HT-018R	REVISION:	00