

TICKET NUMBER	LENGTH	HEIGHT	WIDTH	THICKNESS	QUANTITY
IC-002	1724	287		365	

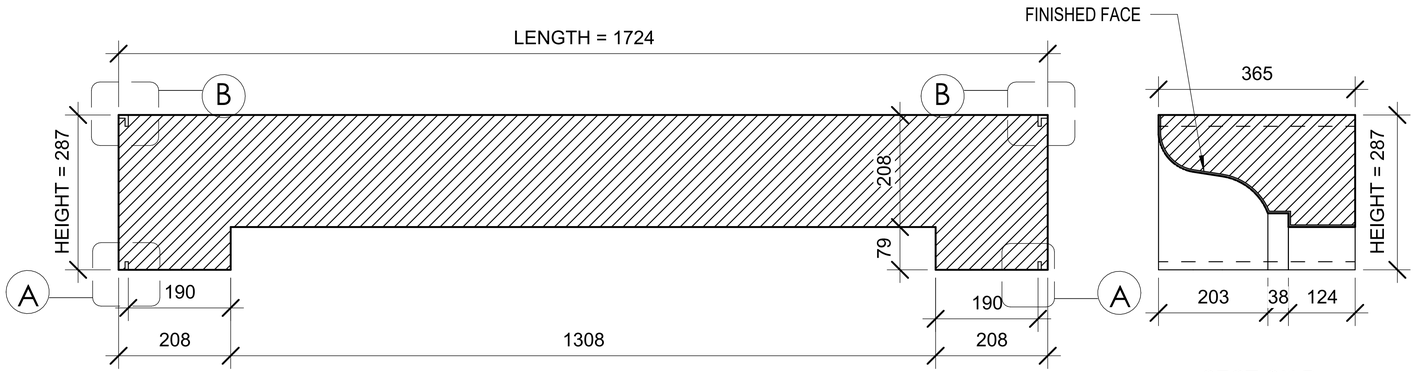


SECTION A


SECTION B

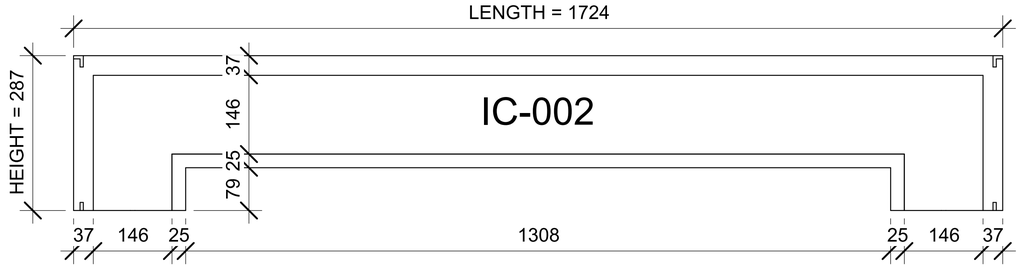


ELEVATION

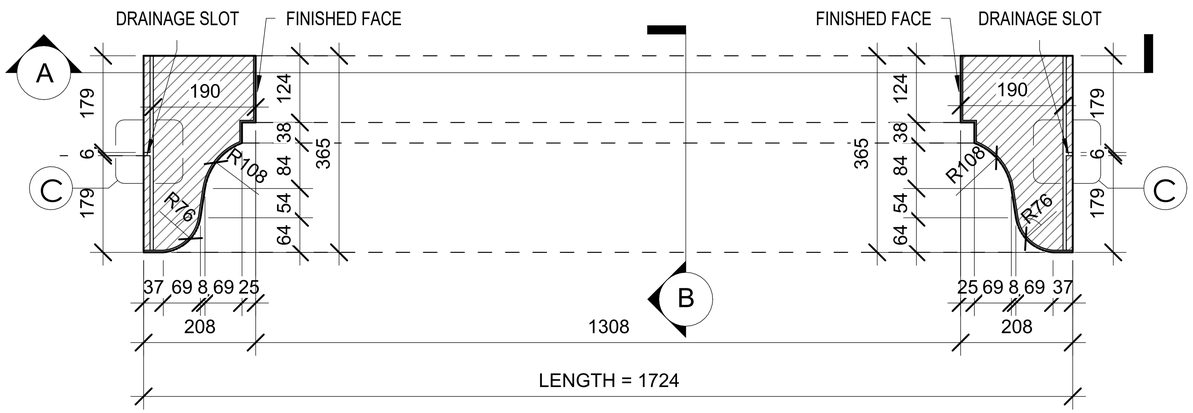


PLAN

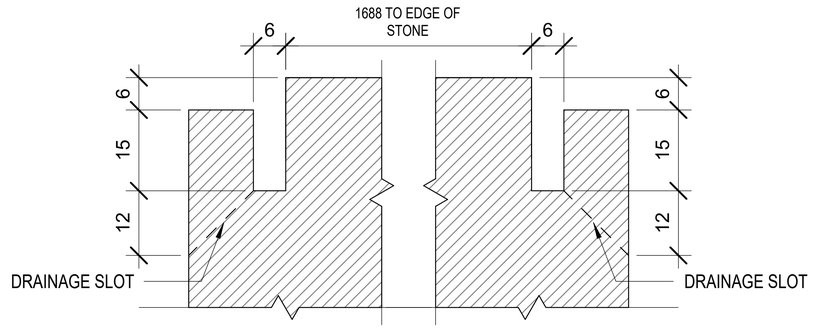

DETAIL B - REBATED KERF (thick stone)

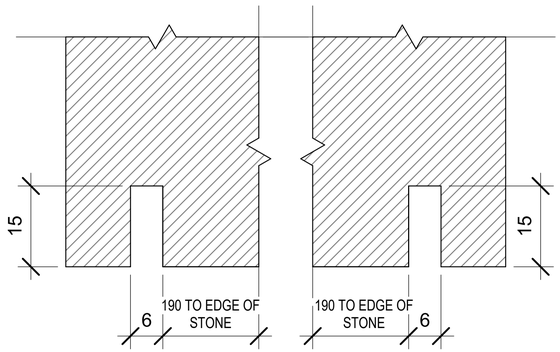

DETAIL A - KERF (thick stone)

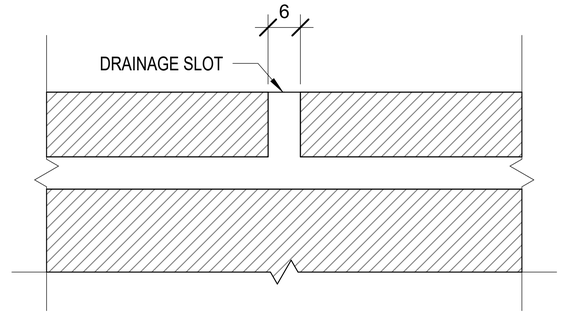

DETAIL C - DRAINAGE SLOT

Rev.	Date	By	Description
00	2025.10.02	-	STONE TICKET PACKAGE P1-P4 For Production
01	2025.11.04	-	STONE TICKET PACKAGE P1-P4 For Production
03	2025.11.12		STONE TICKET PACKAGE P1-P4 and P7 For Production
	2025.12.24		STONE TICKET PACKAGE P1-P4 and P7 For Production

TOLERANCE:		INHABIT GROUP	
		http://www.inhabitgroup.com	
		© Copyright	
PROJECT No:	0001		
CLIENT:	ECLAD		
DRAWN BY:	Pattarapon P.	**CHECKED BY:**	Dararat P.
SCALE:	Not To Scale	**DATE:**	24/12/25

MATERIAL:	Blanco Cristal	**FINISH:**	Honed
PROJECT:	VANCOUVER WASHINGTON TEMPLE		
TICKET NUMBER:	IC-002	**REVISION:**	02