



TICKET NUMBER	LENGTH	HEIGHT	WIDTH	THICKNESS	QUANTITY
OC-007	1367	47	1367	436	

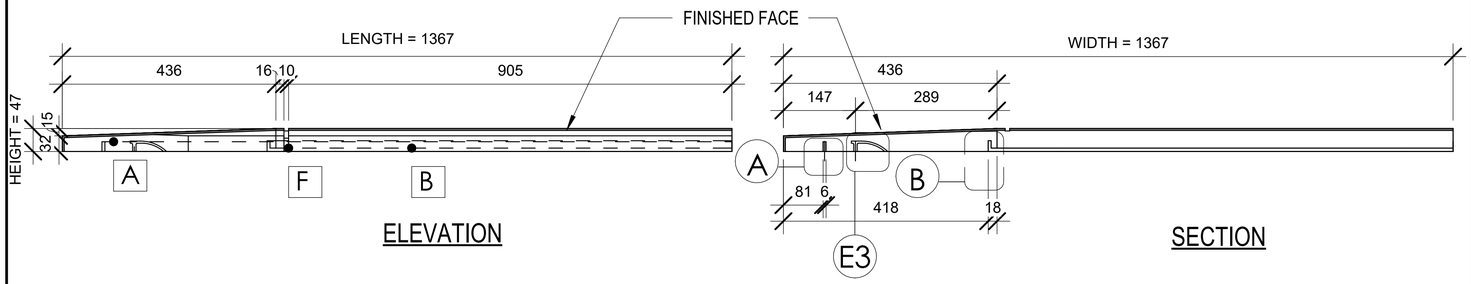

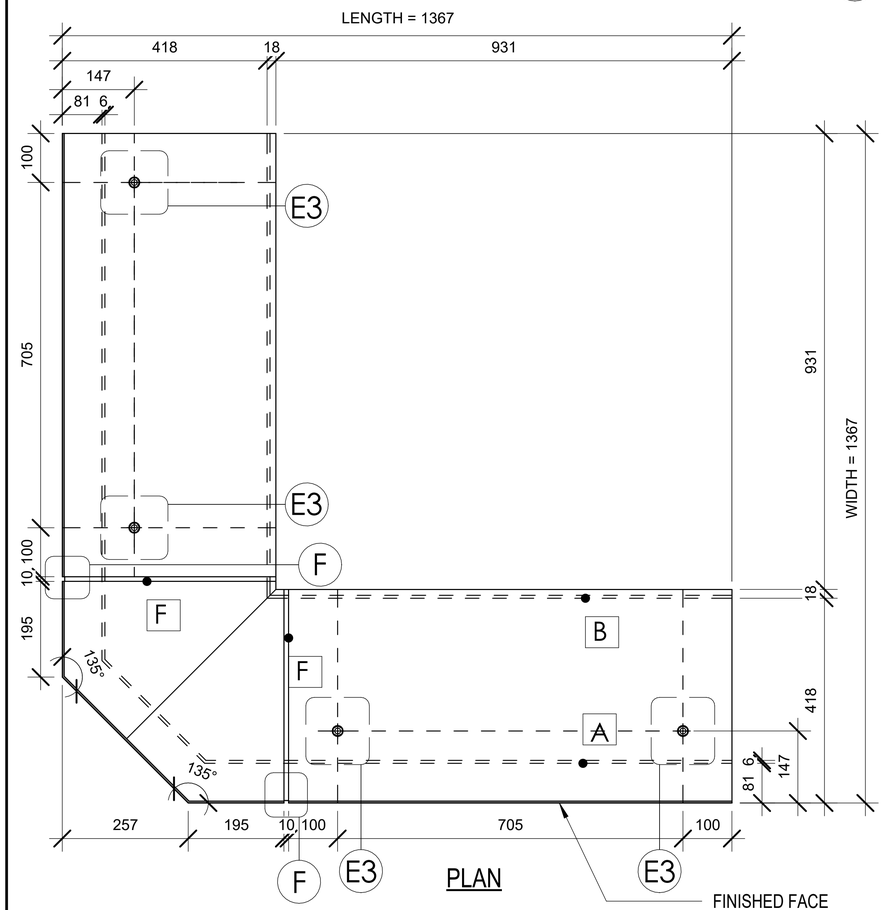


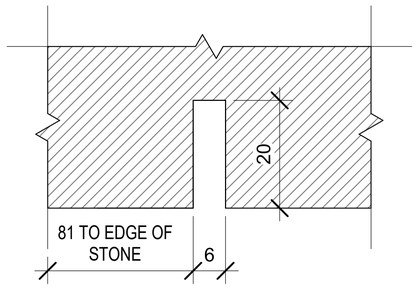


DETAIL A - KERF (with SSC0 clips)

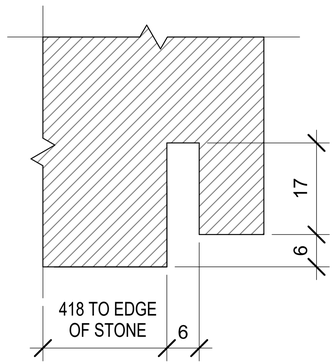


DETAIL B - REBATED KERF (thick stone)

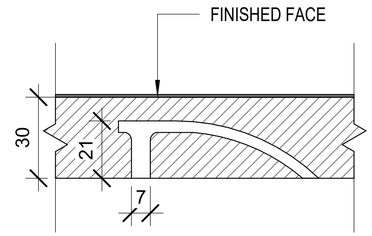

DETAIL E3 - T-31 ANCHOR HOLE (30mm thick stone) - ¼" dia x ¾" deep

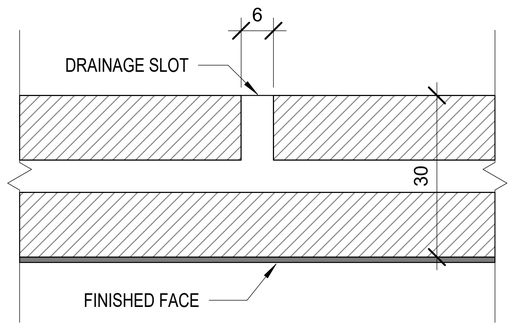

DETAIL C - DRAINAGE SLOT

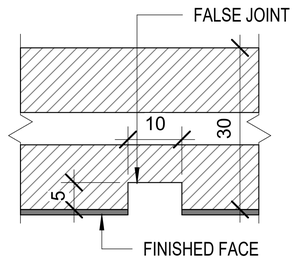

DETAIL F - FALSE JOINT

Rev.	Date	By	Description
04	2025.12.04		STONE TICKET PACKAGE P5 and P7 For Production
06	2025.12.24		STONE TICKET PACKAGE P1-P4 and P7 For Production

TOLERANCE:		INHABIT GROUP	
		http://www.inhabitgroup.com	
		© Copyright	
PROJECT No:	0001		
CLIENT:	ECLAD		
DRAWN BY:	Dararat P.	**CHECKED BY:**	Dararat P.
SCALE:	Not To Scale	**DATE:**	24/12/25

MATERIAL:	Blanco Cristal	**FINISH:**	Honed
PROJECT:	VANCOUVER WASHINGTON TEMPLE		
TICKET NUMBER:	OC-007	**REVISION:**	01