


TICKET NUMBER	LENGTH	HEIGHT	WIDTH	THICKNESS	QUANTITY
OT-004	796	47		340	

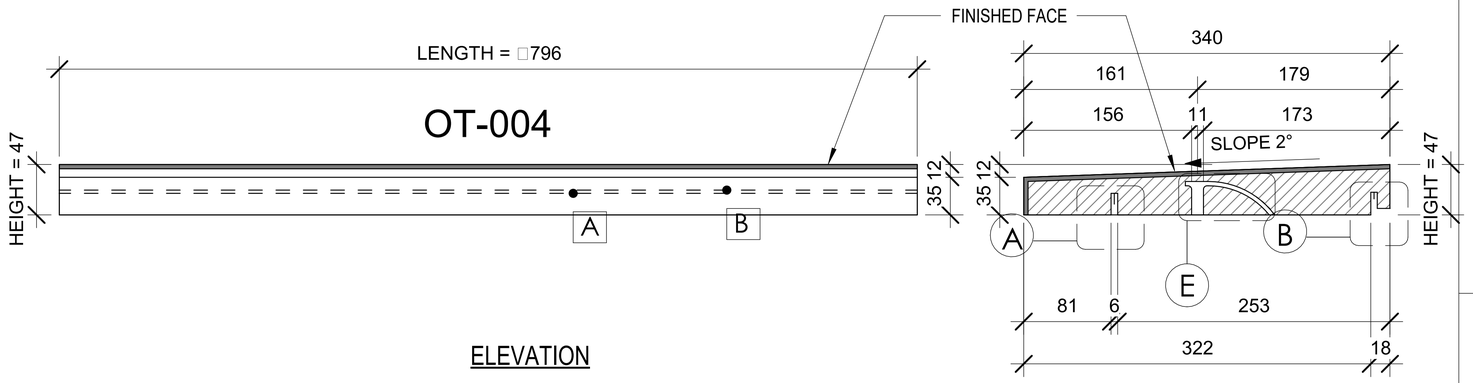


ELEVATION

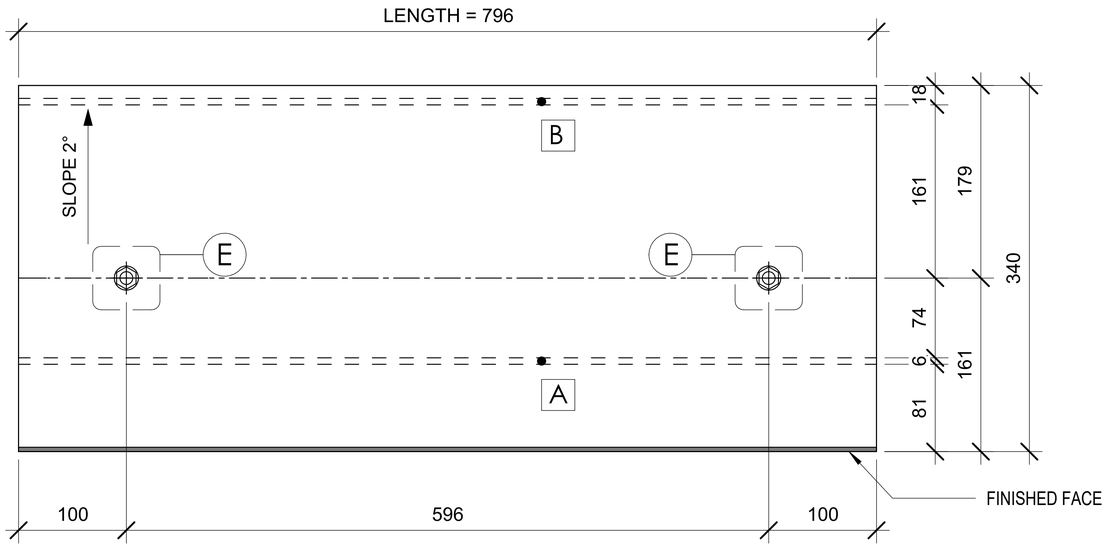


PLAN

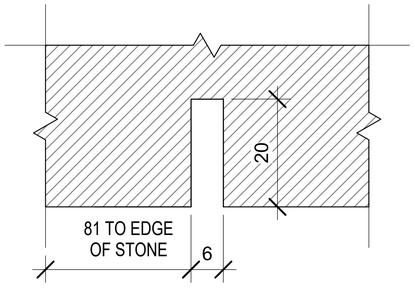

DETAIL A - KERF (with SSC0 clips)

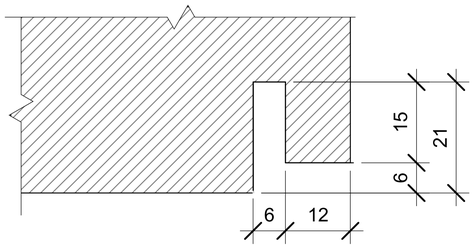

DETAIL B - KERF (with SSC0 clips)

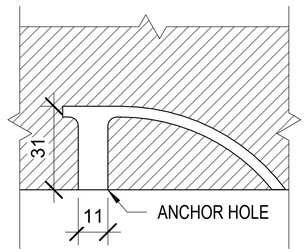

DETAIL E - T-31 ANCHOR HOLE - 3/8” dia x 1¼” deep

Rev.	Date	By	Description
00	2025.10.02	-	STONE TICKET PACKAGE P1-P4 For Production
01	2025.11.04	-	STONE TICKET PACKAGE P1-P4 For Production
06	2025.12.24		STONE TICKET PACKAGE P1-P4 and P7 For Production

TOLERANCE:		INHABIT GROUP	
PROJECT No:	0001	http://www.inhabitgroup.com	
CLIENT:	ECLAD	© Copyright	
DRAWN BY:	Natthapol K.	CHECKED BY:	Dararat P.
SCALE:	Not To Scale	DATE:	24/12/25

MATERIAL:	Blanco Cristal	FINISH:	Honed
PROJECT:	VANCOUVER WASHINGTON TEMPLE		
TICKET NUMBER:	OT-004	REVISION:	02