

TICKET NUMBER	LENGTH	HEIGHT	WIDTH	THICKNESS	QUANTITY
QT-007	1727	201	0	42	

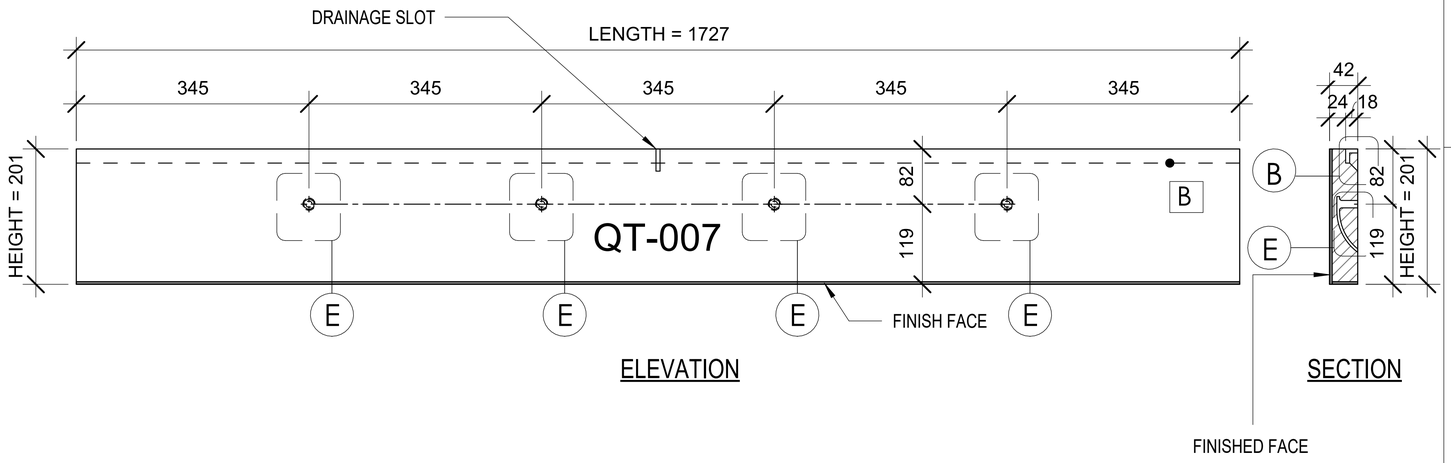


ELEVATION


SECTION

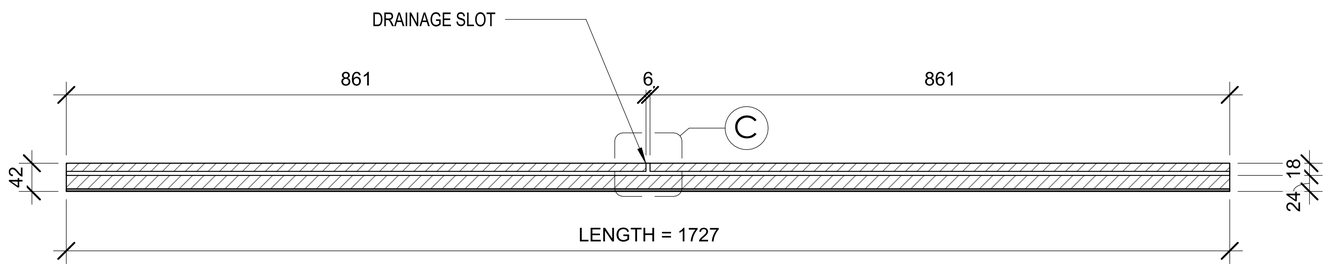


PLAN

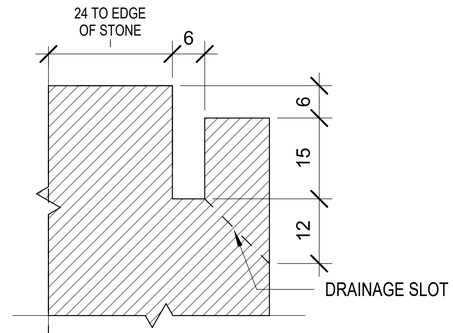

DETAIL B - REBATED KERF (thick stone)

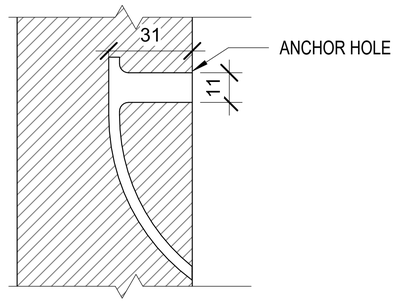

DETAIL E - T-31 ANCHOR HOLE - 3/8" dia x 1¼" deep

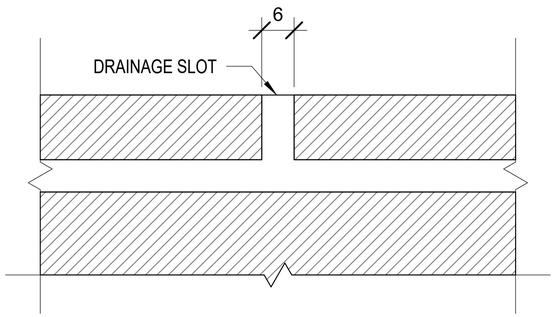

DETAIL C - DRAINAGE SLOT

Rev.	Date	By	Description
10	2026.04.24		STONE TICKET PACKAGE P5 and P8 For Production

TOLERANCE:		INHABIT GROUP	
		http://www.inhabitgroup.com	
		© Copyright	
PROJECT No:	0001		
CLIENT:	ECLAD		
DRAWN BY:	Natthapol K.	**CHECKED BY:**	Dararat P.
SCALE:	Not To Scale	**DATE:**	24/04/26

MATERIAL:	Blanco Cristal	**FINISH:**	Honed
PROJECT:	VANCOUVER WASHINGTON TEMPLE		
TICKET NUMBER:	QT-007	**REVISION:**	00